



094502067888 +239812064282

CHECKED BY
ARCH CHARLSE TAYO



CHECKED BY
ARCH CHARLSE TAYO

201807071958 - 2018120150282


CLIENT;
MR OKUNOWO OMOLADE TOSIN.

PROJECT;

PROPOSED RESIDENTIAL BUILDING PROJECT
@
22 SUNNY CLOSE,
DELE ADEDUGBE ESTATE,
FORMER WILLIAMS ELLIOT ESTATE,
NEW OKO-OBA, IFAKO-IJAIYE LOCAL GOVT AREA,
LAGOS STATE.

FIRM



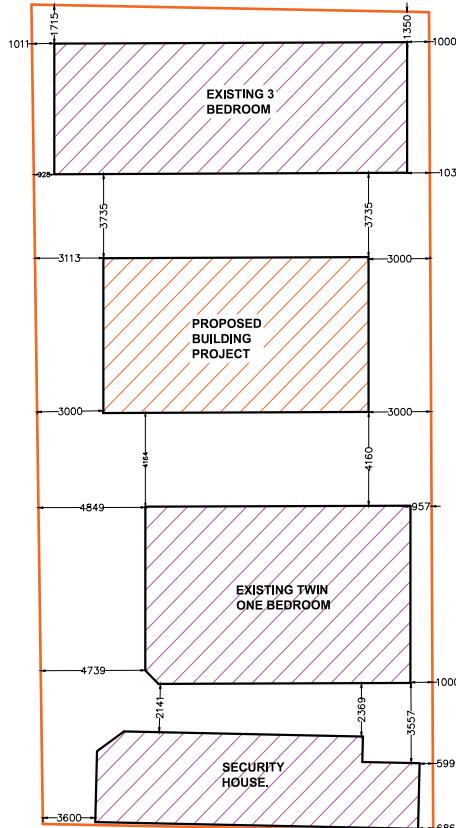

LAND USE ANALYSIS

TOTAL AREA OF SITE	646.290m ²
AREA OF PROPOSED BUILDING.	82.7m ²
AREA OF EXISTING BUILDING.	241.2m ²
50% OF SITE	323.145m ²
NET AREA	322.39m ²
PERCENTAGE COVER	49.88%
VOLUMN	812m ²

SUNNY CLOSE.



GENERAL NOTE.
1. Dimensions are to be read and not scaled.
2. All dimensions and conditions are to be verified on site before proceeding.
3. Drawings from all consultants relating to the same area should be read in conjunction with one another.
4. Should the contractor discern any conflicting information written or drawn, he is to notify the architect immediately.
5. This drawing is subject to world copyright and may not be reproduced in whole or in part for any purpose without prior written consent Allcrownworks.


CLIENT.
MR OKUNOWO OMOLADE TOSIN.

PROJECT NAME AND ADDRESS.
PROPOSED RESIDENTIAL BUILDING PROJECT
@ 22 SUNNY CLOSE,
DELE ADEDUGBE ESTATE,
FORMER WILLIAMS ELLIOT ESTATE,
NEW OKO-OBA,
IFAKO-IIAJYE LOCAL GOVT AREA,
LAGOS STATE.

DRAWING TITLE	SITE LOCATION.
DATE	JANUARY 2024.
DESIGNED BY	ARCH TAYO CHARLES ADEDAPO. TEL: +2348033574252.
DRAWN BY	ALLCROWNWORKS. TEL: +2348071070888, +2348120156282.
CHECKED BY	ARCH TAYO CHARLES ADEDAPO.
SCALE	SCALE TO FIT.
	SHEET A1A

GENERAL NOTE.

NO.	REVISION/ISSUE	DATE

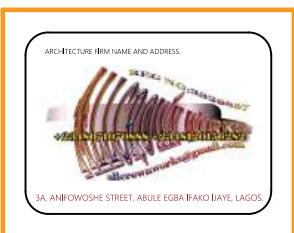

GENERAL NOTE.

1. Dimensions are to be read and not scaled.
2. All dimensions and conditions are to be verified on site before proceeding.
3. Drawings from all consultants relating to the same area should be read in conjunction with one another.
4. Should the contractor discern any conflicting information written or drawn, he is to notify the architect immediately.
5. This drawing is subject to world copyright and must not be reproduced in whole or in part for any purpose without prior written consent Allcrownwarks.

CLIENT.
MR OKUNOWO OMOLADE TOSIN.

PROJECT NAME AND ADDRESS.
PROPOSED RESIDENTIAL BUILDING PROJECT @ 22 SUNNY CLOSE, DELE ADENUGBE ESTATE, FORMER WILLIAMS ELLIOT ESTATE, NEW OKO-OBA, IFAKO-IIAJA LOCAL GOVT AREA, LAGOS STATE.

DRAWING TITLE	SITE LOCATION.
DATE	JANUARY 2024.
DESIGNED BY	ARCH TAYO CHARLES ADEDAPO. TEL: +2348033574252.
DRAWN BY	ALLCROWNWORKS. TEL: +234807070088, +2348120156282.
CHECKED BY	ARCH TAYO CHARLES ADEDAPO.
SCALE	SCALE TO FIT.
	SHEET A1

GENERAL NOTE.			
NO.	REVISION ISSUE	DATE	



ARCHITECTURE FIRM NAME AND ADDRESS

GENERAL NOTE

- Dimensions are to be read and not scaled.
- All dimensions are in metres.
- Drawings from all consultants relating to the same project should be read in conjunction with this drawing.
- Should any conflict arise between this drawing and any other drawing, the architect's drawing shall prevail.
- The drawing is subject to world copyright and may not be reproduced in whole or in part for any purpose without prior written consent of the architect.

ARCHITECTURE FIRM NAME AND ADDRESS


3A ANDOWE STREET, OGA FAO, VANE, LAGOS



CLIENT:
MR OKUNOMO OMOLADE TOSIN.

PROJECT NAME AND ADDRESS
PROPOSED RESIDENTIAL BUILDING PROJECT
© 22 SUNNY CLOSE,
DELE ADEGIGE ESTATE,
FORMER WILLIAMS ELLIO ESTATE,
NEW OGOGO, OGBA, LAGOS STATE,
IFAKO SHARIE, LOCAL GOVT AREA,
LAGOS STATE.

DRAWING TITLE	GROUND FLOOR PLAN
DATE	JANUARY 2024.
DESIGNED BY	ARCH TATO CHARLES ADEDAPO. TEL: +2348033121622.
DRAWN BY	ALLCROWNWORKS. TEL: +2348033121622.
CHECKED BY	ARCH TATO CHARLES ADEDAPO.
SCALE	SCALE TO FIT.
SHEET	A3

NO.	REVISION/ISSUE	DATE

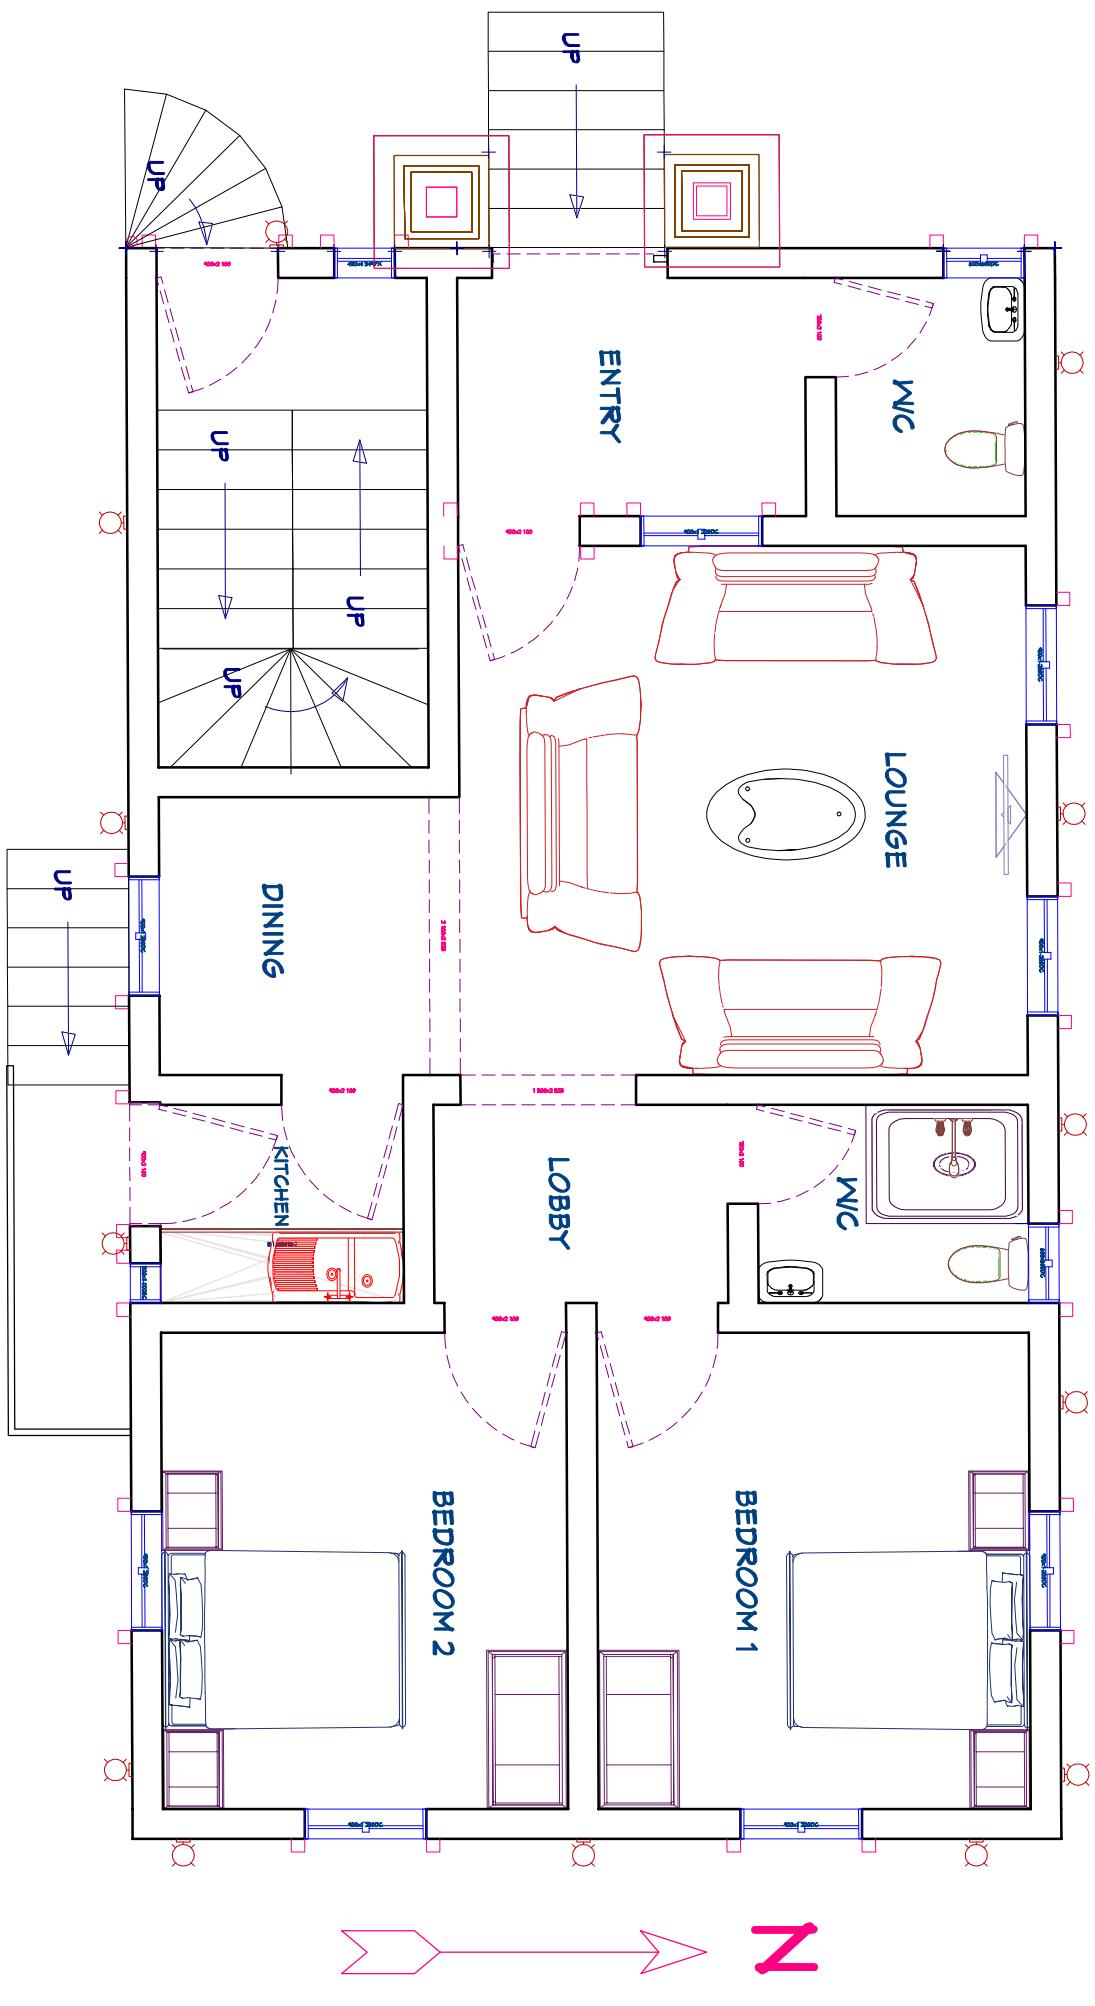

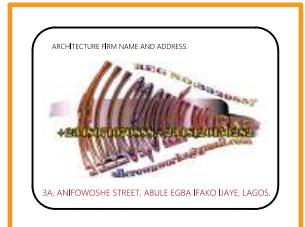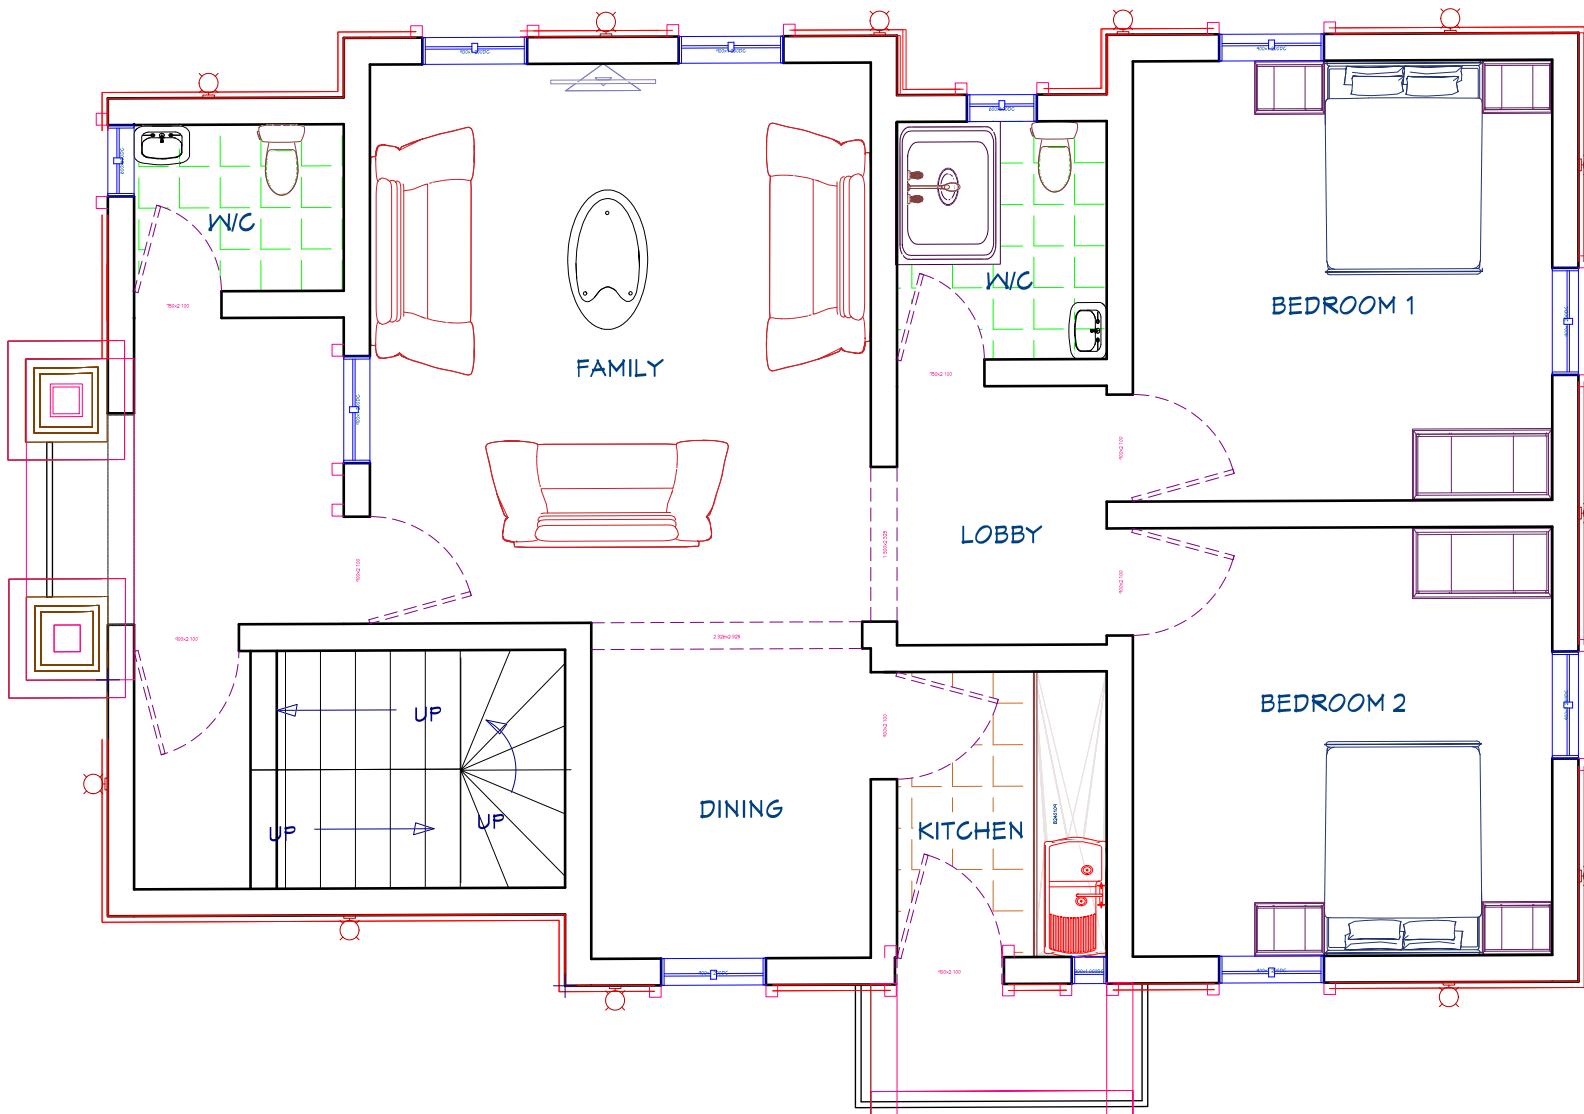

GENERAL NOTE.

1. Dimensions are to be read and not scaled.
2. All dimensions and conditions are to be verified on site before proceeding.
3. Drawings from all consultants relating to the same area should be read in conjunction with one another.
4. Should the contractor discern any conflicting information written or drawn, he is to notify the architect immediately.
5. This drawing is subject to world copyright and may not be reproduced in whole or in part for any purpose without prior written consent Allcrownworks.


CLIENT.
MR OKUNOWO OMOLADE TOSIN.

PROJECT NAME AND ADDRESS.
PROPOSED RESIDENTIAL BUILDING PROJECT
@ 22 SUNNY CLOSE,
DELE ADEDUBU ESTATE,
FORMER WILLIAMS ELLIOT ESTATE,
NEW OKO-OBA,
IFAKO-JAIYE LOCAL GOVT AREA,
LAGOS STATE.

DRAWING TITLE	FIRST FLOOR PLAN.	
DATE	JANUARY 2024.	
DESIGNED BY	ARCH TAYO CHARLES ADEDAPO. TEL: +2348033574252.	
DRAWN BY	ALLCROWNWORKS. TEL: +2348071070888, +2348120156282.	
CHECKED BY	ARCH TAYO CHARLES ADEDAPO.	
SCALE	SCALE TO FIT.	SHEET A4

GENERAL NOTE.

NO.	REVISION/ISSUE	DATE
-----	----------------	------

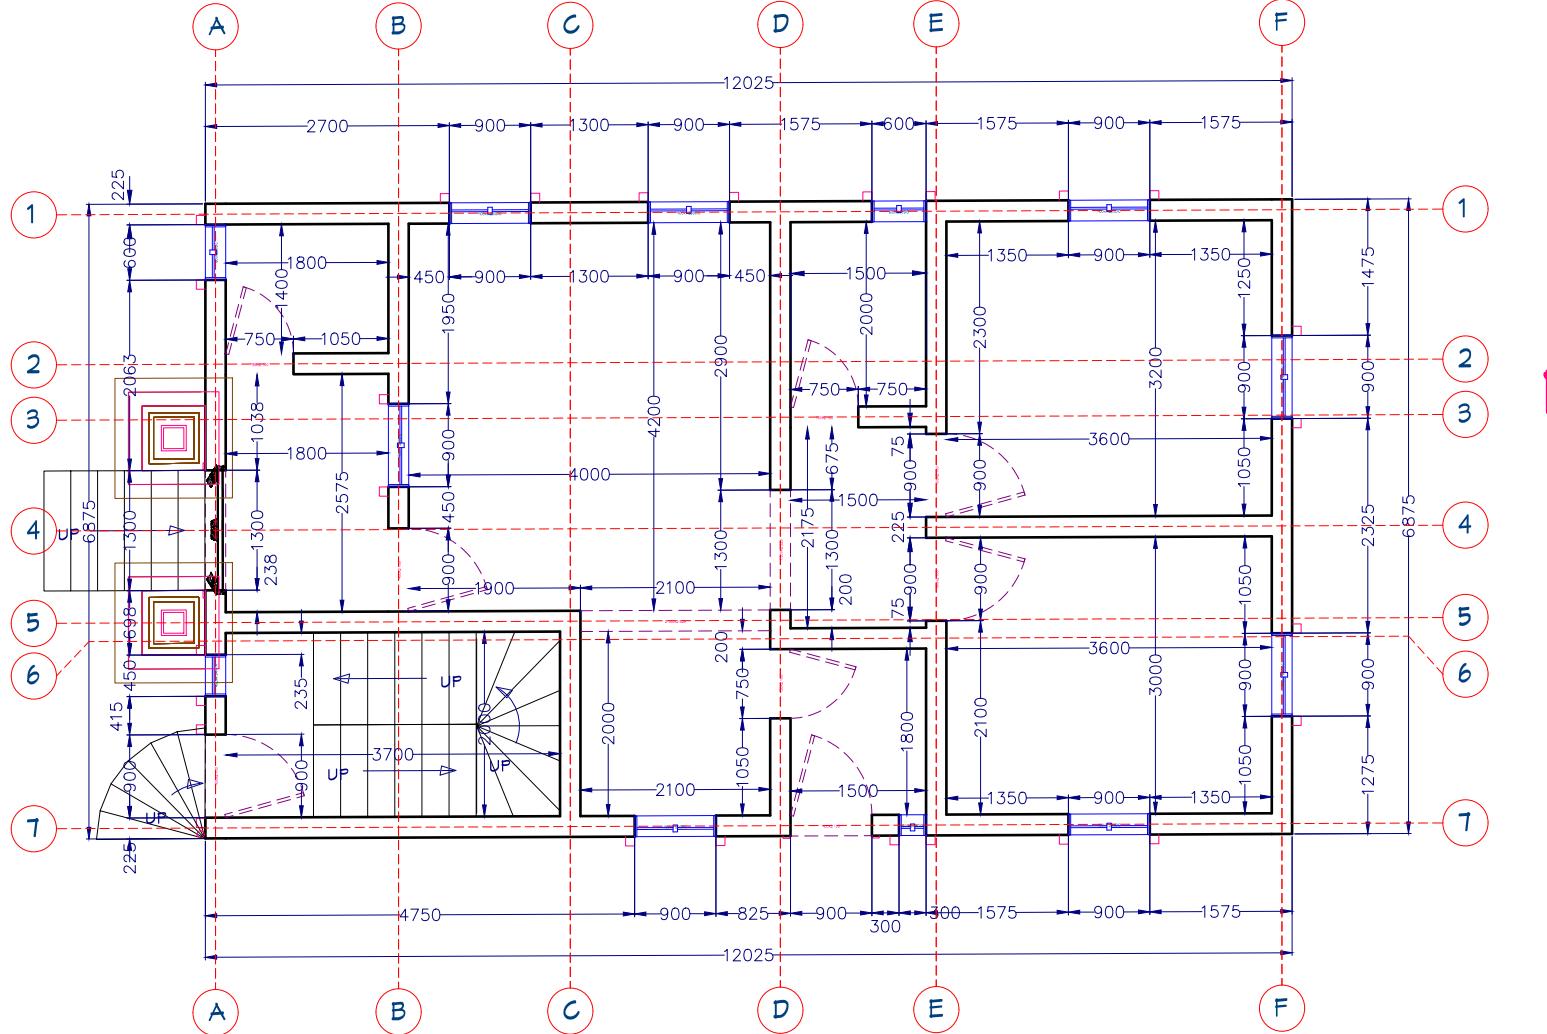

GENERAL NOTE:

- Dimensions are to be read and not scaled.
- All dimensions and conditions are to be verified on site before proceeding.
- Drawings from all consultants relating to the same area should be read in conjunction with one another.
- Should the contractor discern any conflicting information written or drawn, he is to notify the architect immediately.
- This drawing is subject to world copyright and may not be reproduced in whole or in part for any purpose without prior written consent Allcrownworks.


CLIENT:
MR OKUNOWO OMOLADE TOSIN.

PROJECT NAME AND ADDRESS:
PROPOSED RESIDENTIAL BUILDING PROJECT
@ 22 SUNNY CLOSE,
DELE ADEDUGBE ESTATE,
FORMER WILLIAMS ELLIOT ESTATE,
NEW OKO-OBA,
IFAKO-IJAIYE LOCAL GOVT AREA,
LAGOS STATE.

DRAWING TITLE: GROUND FLOOR DIM.	
DATE	JANUARY 2024.
DESIGNED BY	ARCH TAYO CHARLES ADEDAPO. TEL: +2348033574252.
DRAWN BY	ALLCROWNWORKS. TEL: +234807070888, +2348120156282.
CHECKED BY	ARCH TAYO CHARLES ADEDAPO.
SCALE	SCALE TO FIT.
SHEET: A3	

GENERAL NOTE:

NO.	REVISION/ISSUE	DATE

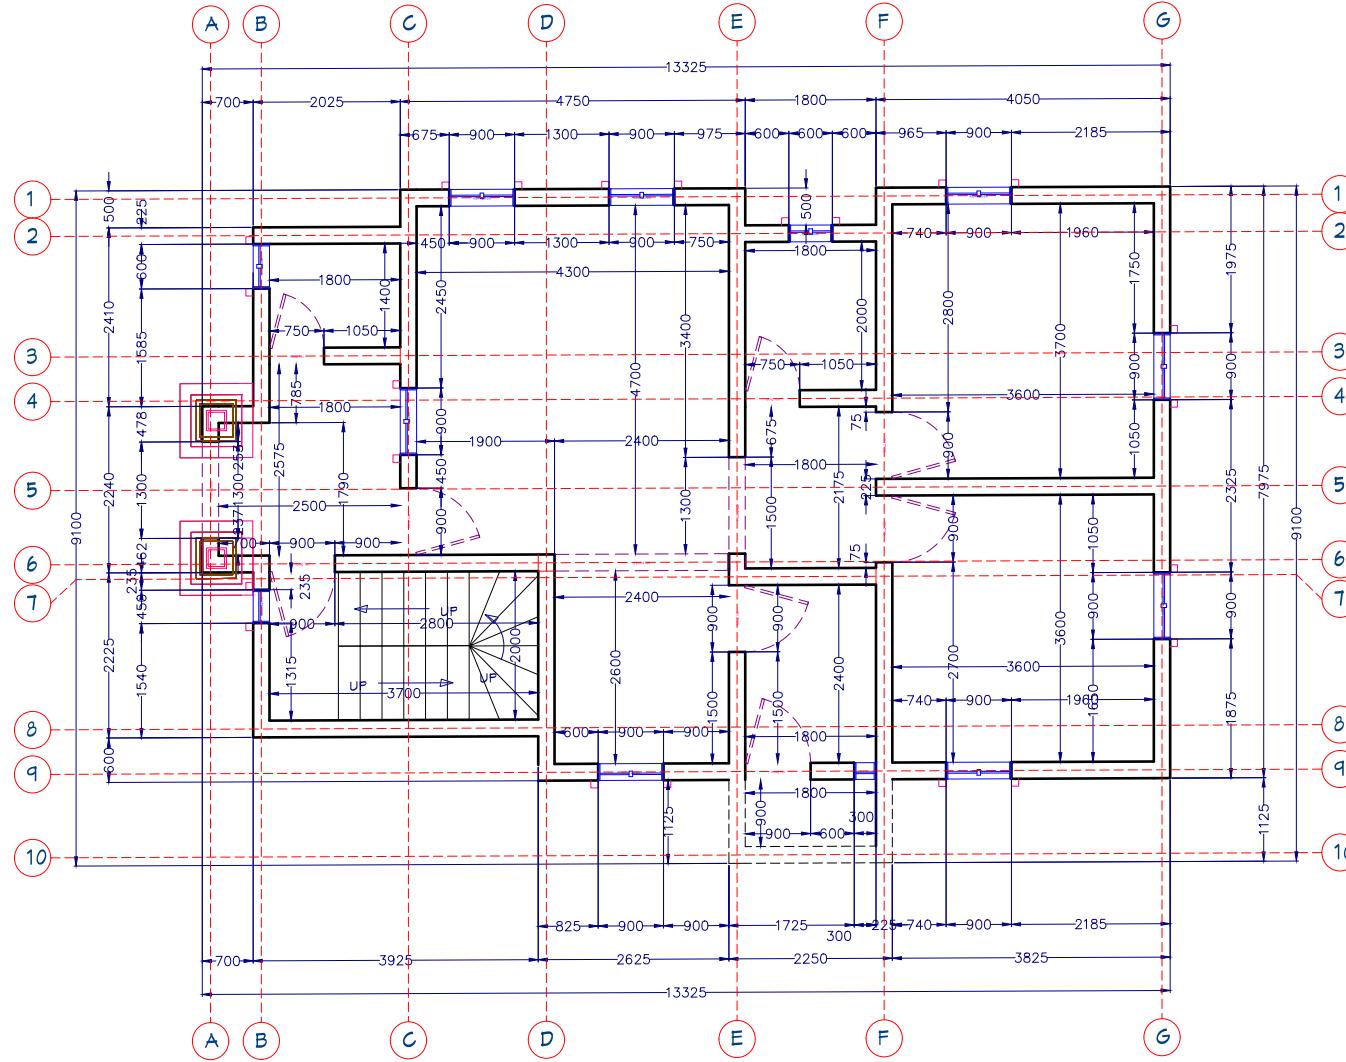

GENERAL NOTE.
 1. Dimensions are to be read and not scaled.
 2. All dimensions and conditions are to be verified on site before proceeding.
 3. Drawings from all consultants relating to the same area should be read in conjunction with one another.
 4. Should the contractor discern any conflicting information written or drawn, he is to notify the architect immediately.
 5. This drawing is subject to world copyright and may not be reproduced in whole or in part for any purpose without prior written consent Allcrownworks.


CLIENT.
MR OKUNOWO OMOLADE TOSIN.

PROJECT NAME AND ADDRESS.
PROPOSED RESIDENTIAL BUILDING PROJECT
@ 22 SUNNY CLOSE,
DELE ADEDUBUKE ESTATE,
FORMER WILLIAMS ELLIOT ESTATE,
NEW OKO-OBA,
IFAKO-IIAJYE LOCAL GOVT AREA,
LAGOS STATE.

DRAWING TITLE	FIRST FLOOR DIM.
DATE	JANUARY 2024.
DESIGNED BY	ARCH TAYO CHARLES ADEDAPO. TEL: +2348033574252.
DRAWN BY	ALLCROWNWORKS. TEL: +234807070888, +2348120156282.
CHECKED BY	ARCH TAYO CHARLES ADEDAPO.
SCALE	SCALE TO FIT.
SHEET A6	

GENERAL NOTE.

NO.	REVISION/ISSUE	DATE

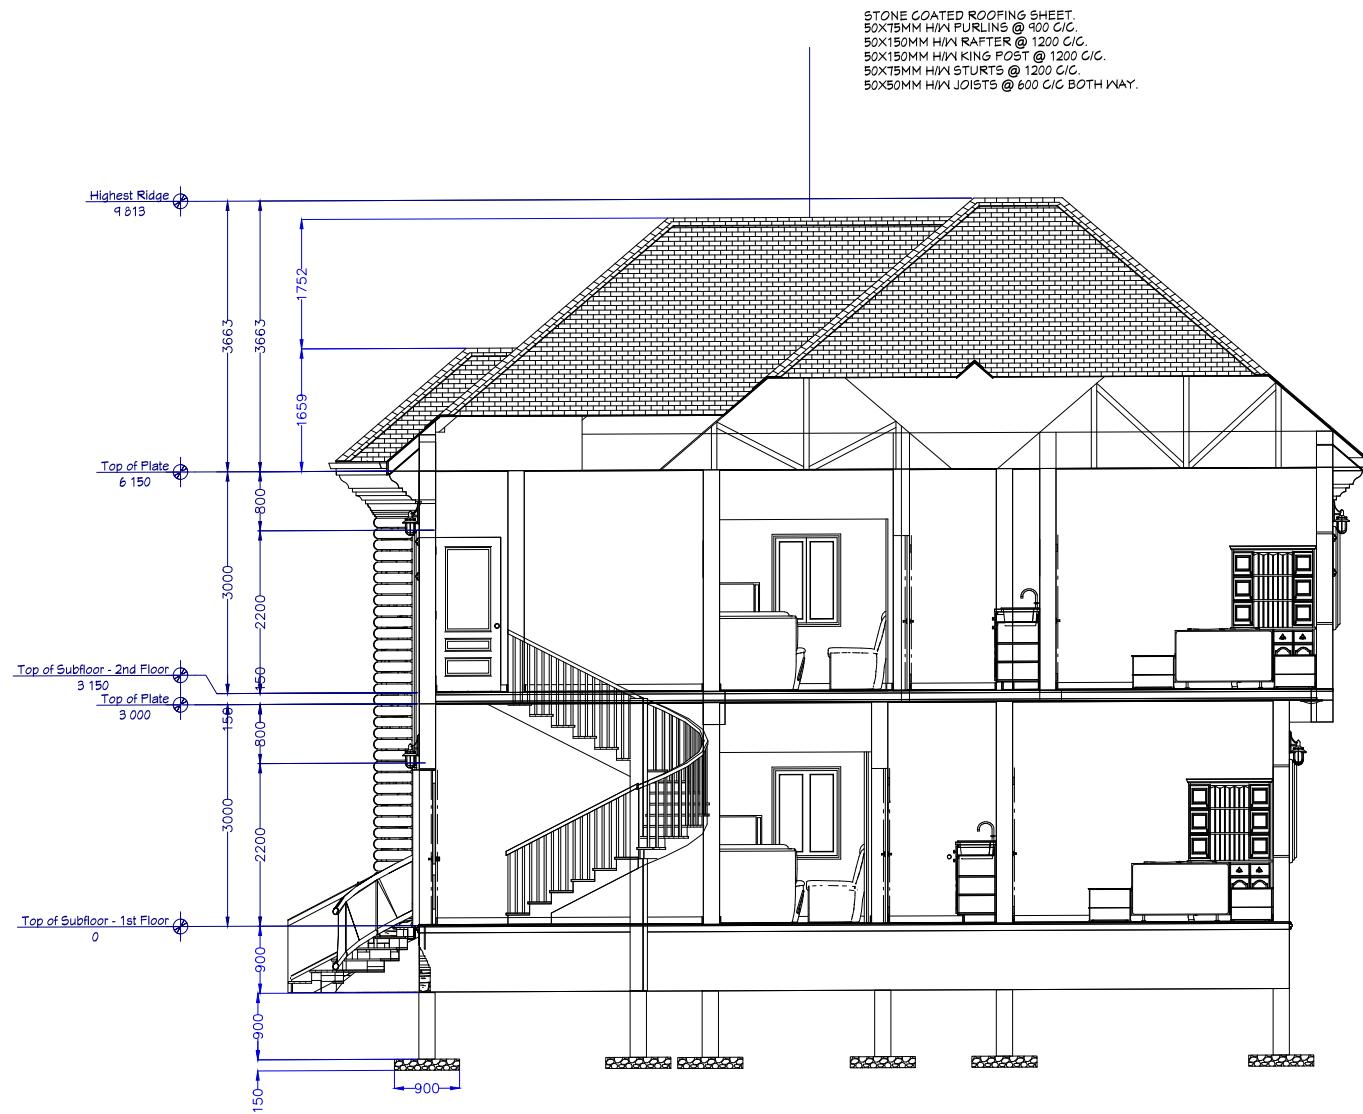

GENERAL NOTE.

- Dimensions are to be read and not scaled.
- All dimensions and conditions are to be verified on site before proceeding.
- Drawings from all consultants relating to the same area should be read in conjunction with one another.
- Should the contractor discern any conflicting information written or drawn, he is to notify the architect immediately.
- This drawing is subject to world copyright and may not be reproduced in whole or in part for any purpose without prior written consent Allcrownworks.


CLIENT.
MR OKUNOWO OMOLADE TOSIN.

PROJECT NAME AND ADDRESS.
PROPOSED RESIDENTIAL BUILDING PROJECT @
22 SUNNY CLOSE, DELE ADEDUGBE ESTATE, FORMER WILLIAMS ELLIOT ESTATE, NEW OKO-OBA, IFAKO-IIAJYE LOCAL GOVT AREA, LAGOS STATE.

DRAWING TITLE	SECTION X.
DATE	JANUARY 2024.
DESIGNED BY	ARCH TAYO CHARLES ADEDAOPO. TEL: +2348033574252.
DRAWN BY	ALLCROWNWORKS. TEL: +234807070888, +2348120156282.
CHECKED BY	ARCH TAYO CHARLES ADEDAOPO.
SCALE	SCALE TO FIT.
SHEET A7	

GENERAL NOTE.

NO.	REVISION/ISSUE	DATE

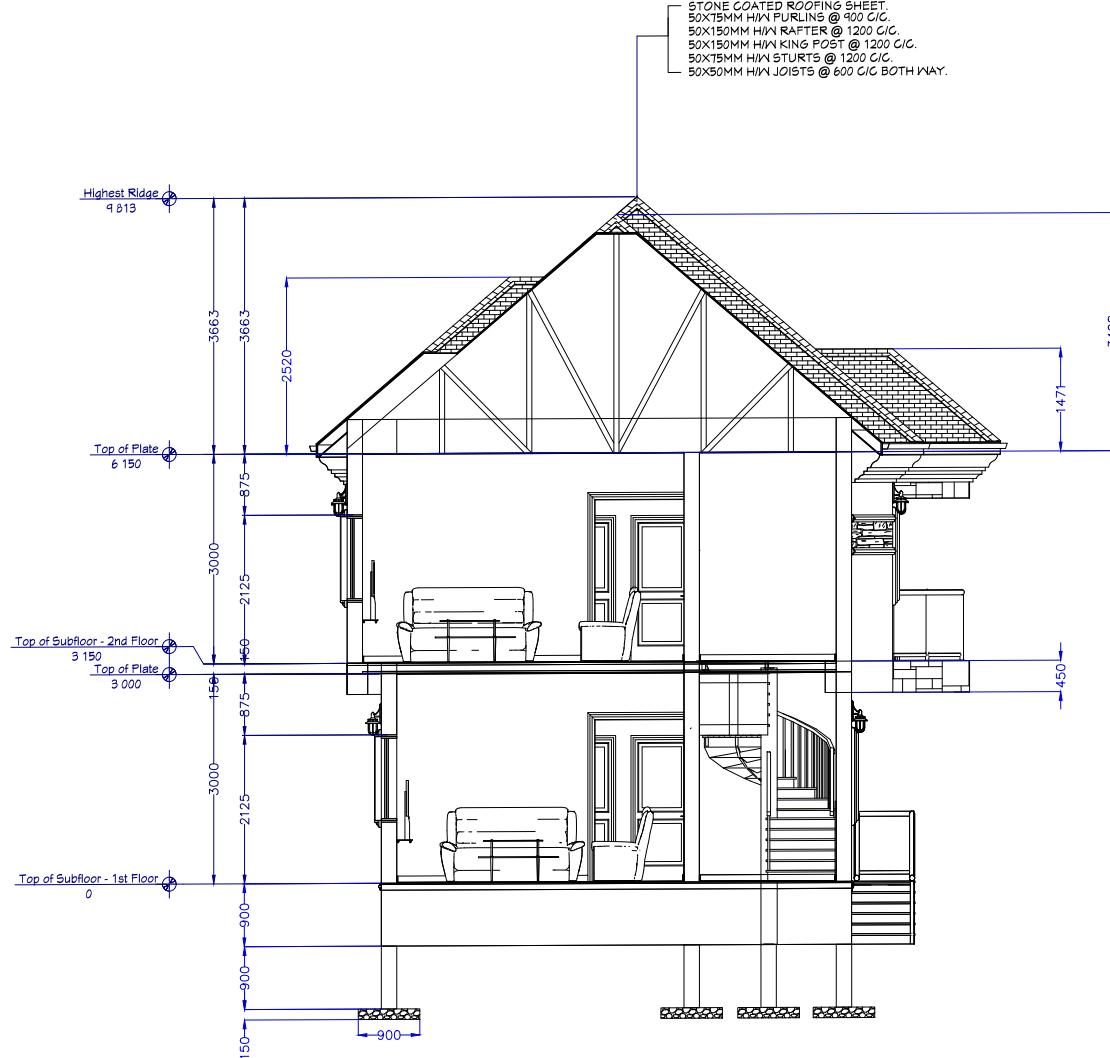

GENERAL NOTE.

- Dimensions are to be read and not scaled.
- All dimensions and conditions are to be verified on site before proceeding.
- Drawings from all consultants relating to the same area should be read in conjunction with one another.
- Should the contractor discern any conflicting information written or drawn, he is to notify the architect immediately.
- This drawing is subject to world copyright and may not be reproduced in whole or in part for any purpose without prior written consent Allcrownworks.


CLIENT.
MR OKUNOWO OMOLADE TOSIN.

PROJECT NAME AND ADDRESS.
PROPOSED RESIDENTIAL BUILDING PROJECT
@ 22 SUNNY CLOSE,
DELE ADEDUGBE ESTATE,
FORMER WILLIAMS ELLIOT ESTATE,
NEW OKO-OBA,
IFAKO-IJAYE LOCAL GOVT AREA,
LAGOS STATE.

DRAWING TITLE	SECTION Y.
DATE	JANUARY 2024.
DESIGNED BY	ARCH TAYO CHARLES ADEDAPO. TEL: +2348033574252.
DRAWN BY	ALLCROWNWORKS. TEL: +234807070888, +2348120156282.
CHECKED BY	ARCH TAYO CHARLES ADEDAPO.
SCALE	SCALE TO FIT.
SHEET A8	

GENERAL NOTE.

NO.	REVISION/ISSUE	DATE

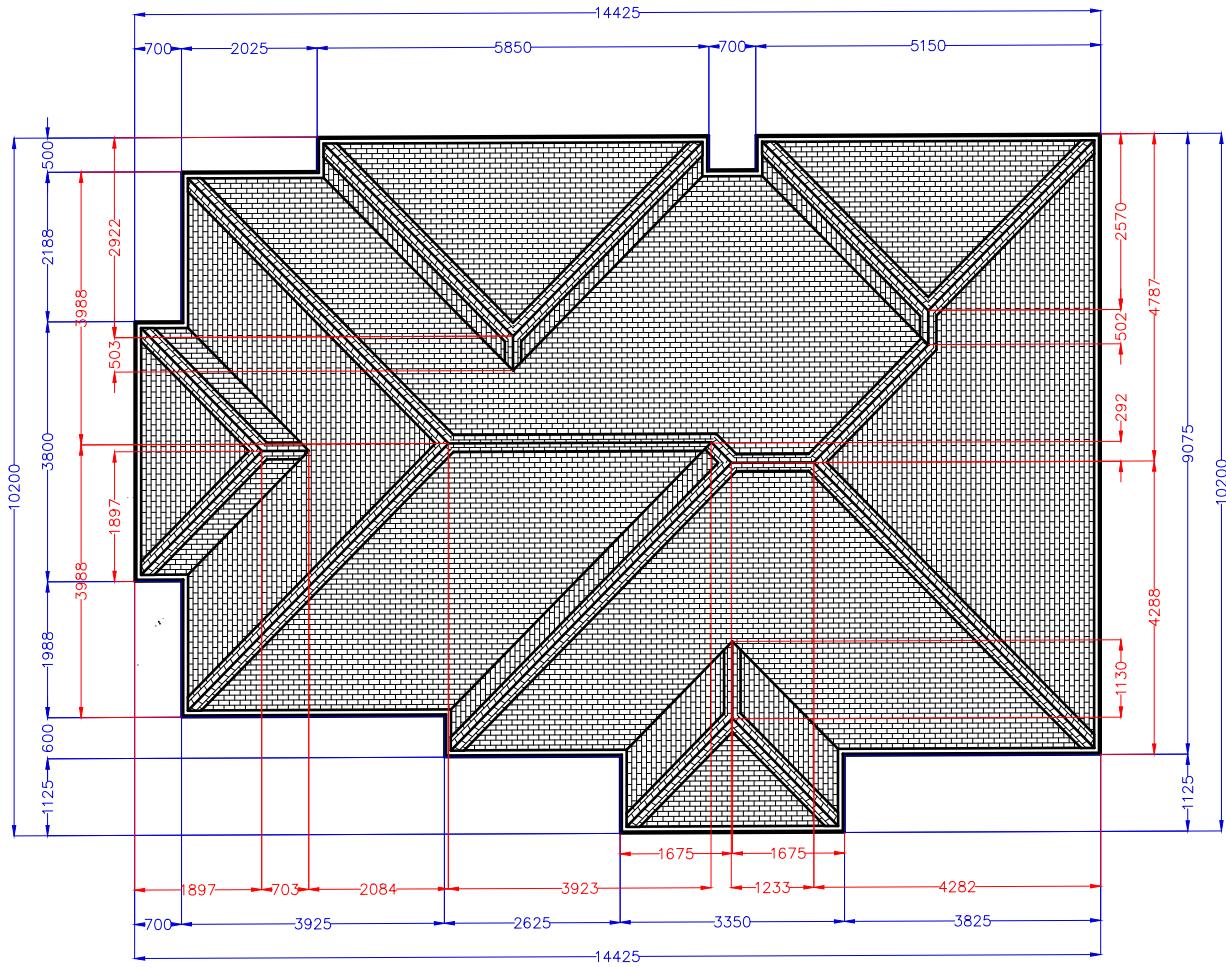

GENERAL NOTE.

- Dimensions are to be read and not scaled.
- All dimensions and conditions are to be verified on site before proceeding.
- Drawings from all consultants relating to the same area should be read in conjunction with one another.
- Should the contractor discern any conflicting information written or drawn, he is to notify the architect immediately.
- This drawing is subject to world copyright and may not be reproduced in whole or in part for any purpose without prior written consent Allcrownworks.

CLIENT.

MR OKUNOWO OMOLADE TOSIN.

PROJECT NAME AND ADDRESS.

PROPOSED RESIDENTIAL BUILDING PROJECT

@ 22 SUNNY CLOSE,
DELE ADEDUGBE ESTATE,
FORMER WILLIAMS ELLIOT ESTATE,
NEW OKO-OBA,
IFAKO-IIAJYE LOCAL GOVT AREA,
LAGOS STATE.

DRAWING TITLE	ROOF.
DATE	JANUARY 2024.
DESIGNED BY	ARCH TAYO CHARLES ADEDAPO. TEL: +2348033574252.
DRAWN BY	ALLCROWNWORKS. TEL: +234807070888, +2348120156282.
CHECKED BY	ARCH TAYO CHARLES ADEDAPO.
SCALE	SCALE TO FIT.
SHEET A9	

GENERAL NOTE.

NO.	REVISION/ISSUE	DATE



ARCHITECTURE ITEM NAME AND ADDRESS.

3A, ANIFOWOSHE STREET, ABULE EGBA IFAKO IJAYE, LAGOS

GENERAL NOTE.
1. Dimensions are to be read and not scaled.
2. All dimensions and conditions are to be verified on site before proceeding.
3. Drawings from all consultants relating to the same area should be read in conjunction with one another.
4. Should the contractor discern any conflicting information written or drawn, he is to notify the architect immediately.
5. This drawing is subject to world copyright and may not be reproduced in whole or in part for any purpose without prior written consent Allcrownworks.

CLIENT.


MR OKUNOWO OMOLADE TOSIN.

PROJECT NAME AND ADDRESS.

PROPOSED RESIDENTIAL BUILDING PROJECT
@
22 SUNNY CLOSE,
DELE ADEDUGBE ESTATE,
FORMER WILLIAMS ELLIOT ESTATE,
NEW OKO-OBA,
IFAKO-IJAYE LOCAL GOVT AREA,
LAGOS STATE.

DRAWING TITLE	FRONT SIDE VIEW.
DATE	JANUARY 2024.
DESIGNED BY	ARCH TAYO CHARLES ADEDAPO. TEL: +2348033574252.
DRAWN BY	ALLCROWNWORKS. TEL: +2348071070888, +2348120156282.
CHECKED BY	ARCH TAYO CHARLES ADEDAPO.
SCALE	SCALE TO FIT.
	SHEET A10

NO.	REVISION/ISSUE	DATE

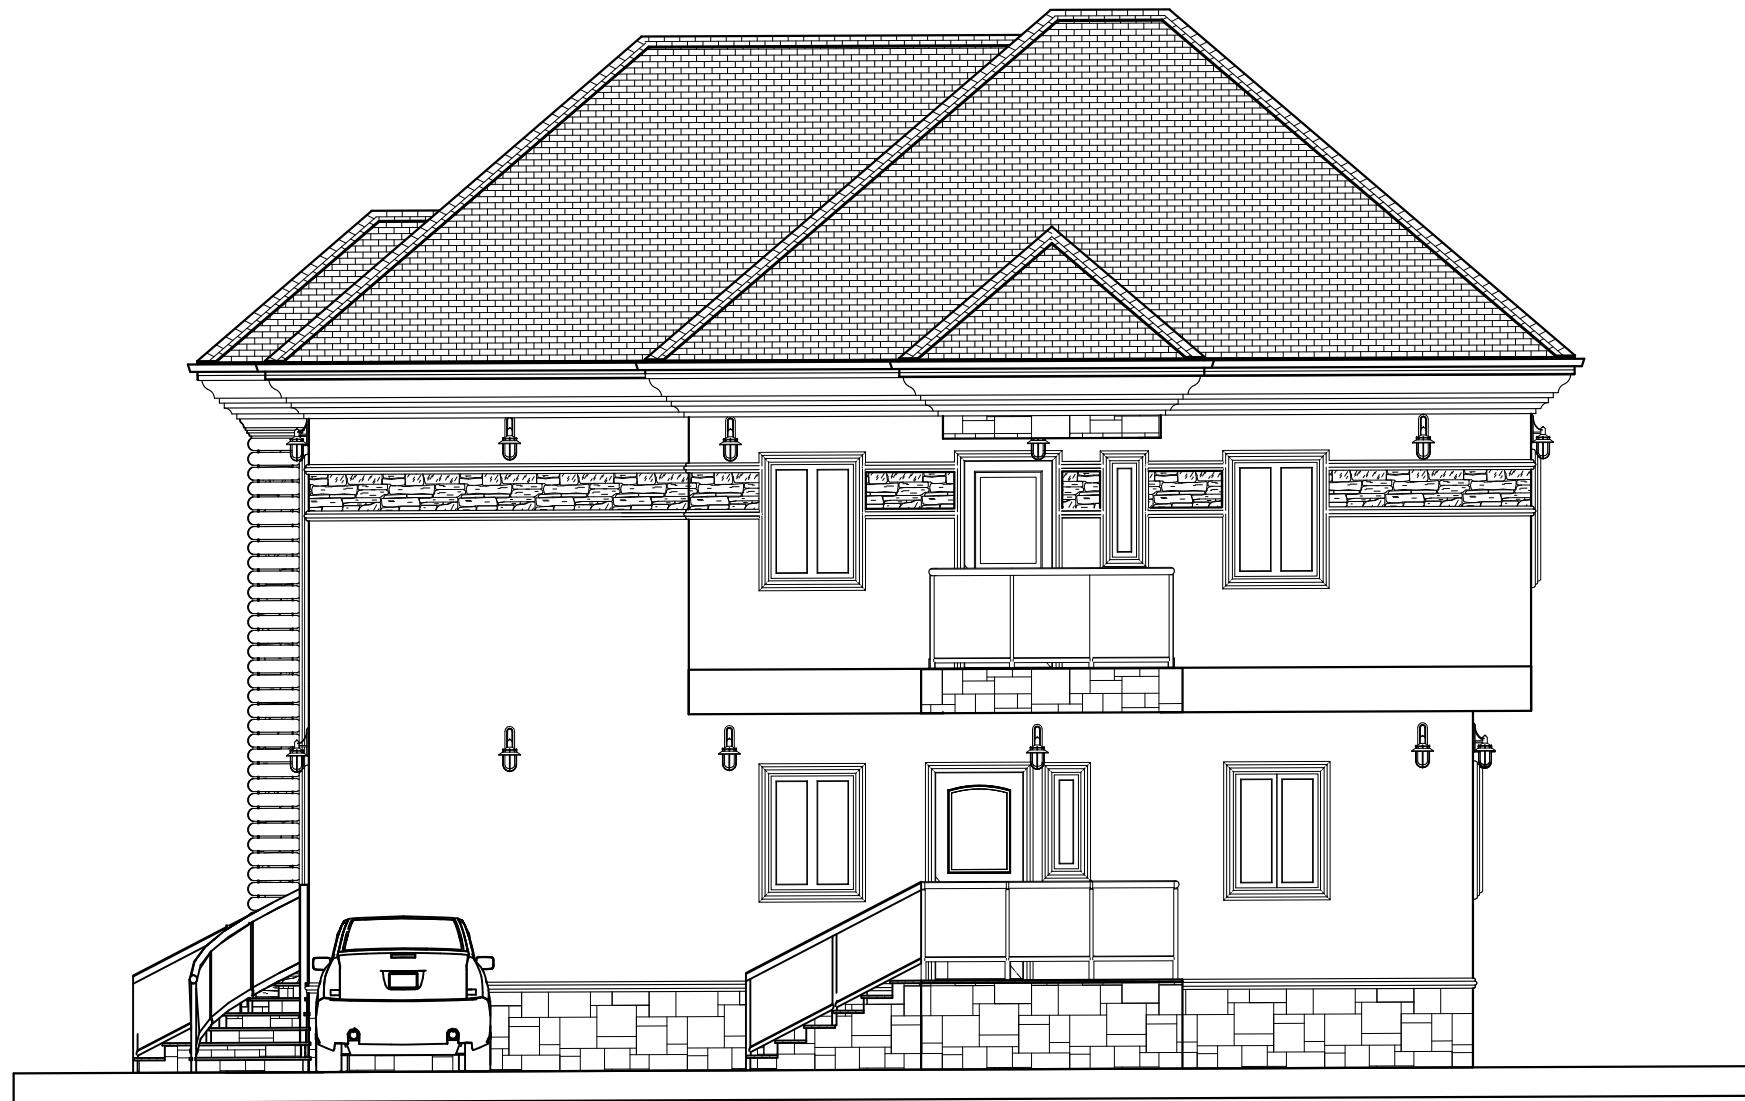

GENERAL NOTE.

1. Dimensions are to be read and not scaled.
2. All dimensions and conditions are to be verified on site before proceeding.
3. Drawings from all consultants relating to the same area should be read in conjunction with one another.
4. Should the contractor discern any conflicting information written or drawn, he is to notify the architect immediately.
5. This drawing is subject to world copyright and may not be reproduced in whole or in part for any purpose without prior written consent Allcrownworks.

CLIENT.

MR OKUNOWO OMOLADE TOSIN.

PROJECT NAME AND ADDRESS.

PROPOSED RESIDENTIAL BUILDING PROJECT
@
22 SUNNY CLOSE,
DELE ADEDUGBE ESTATE,
FORMER WILLIAMS ELLIOT ESTATE,
NEW OKO-OBA,
IFAKO-IJAYE LOCAL GOVT AREA,
LAGOS STATE.

DRAWING TITLE **RIGHT SIDE VIEW.**

DATE	JANUARY 2024.
DESIGNED BY	ARCH TAYO CHARLES ADEDAOPO. TEL: +2348033574252.
DRAWN BY	ALLCROWNWORKS. TEL: +2348071070888, +2348120156282.
CHECKED BY	ARCH TAYO CHARLES ADEDAOPO.
SCALE	SCALE TO FIT.
SHEET A11	

GENERAL NOTE.

NO.	REVISION/ISSUE	DATE



ARCHITECTURE FIRM NAME AND ADDRESS.

3A, ANIFOWOSHE STREET, ABULE EGBA IFAKO IJAYE, LAGOS

GENERAL NOTE.

- Dimensions are to be read and not scaled.
- All dimensions and conditions are to be verified on site before proceeding.
- Drawings from all consultants relating to the same area should be read in conjunction with one another.
- Should the contractor discern any conflicting information written or drawn, he is to notify the architect immediately.
- This drawing is subject to world copyright and may not be reproduced in whole or in part for any purpose without prior written consent Allcrownworks.

CLIENT.

MR OKUNOWO OMOLADE TOSIN.


PROJECT NAME AND ADDRESS.

PROPOSED RESIDENTIAL BUILDING PROJECT
@
22 SUNNY CLOSE,
DELE ADEDUBU ESTATE,
FORMER WILLIAMS ELLIOT ESTATE,
NEW OKO-OBA,
IFAKO-IJAYE LOCAL GOVT AREA,
LAGOS STATE.

DRAWING TITLE	LEFT SIDE VIEW.
DATE	JANUARY 2024.
DESIGNED BY	ARCH TAYO CHARLES ADEDAPO. TEL: +2348033574252.
DRAWN BY	ALLCROWNWORKS. TEL: +2348071070888, +2348120156282.
CHECKED BY	ARCH TAYO CHARLES ADEDAPO.
SCALE	SCALE TO FIT.
SHEET	A12

GENERAL NOTE.

NO.	REVISION/ISSUE	DATE

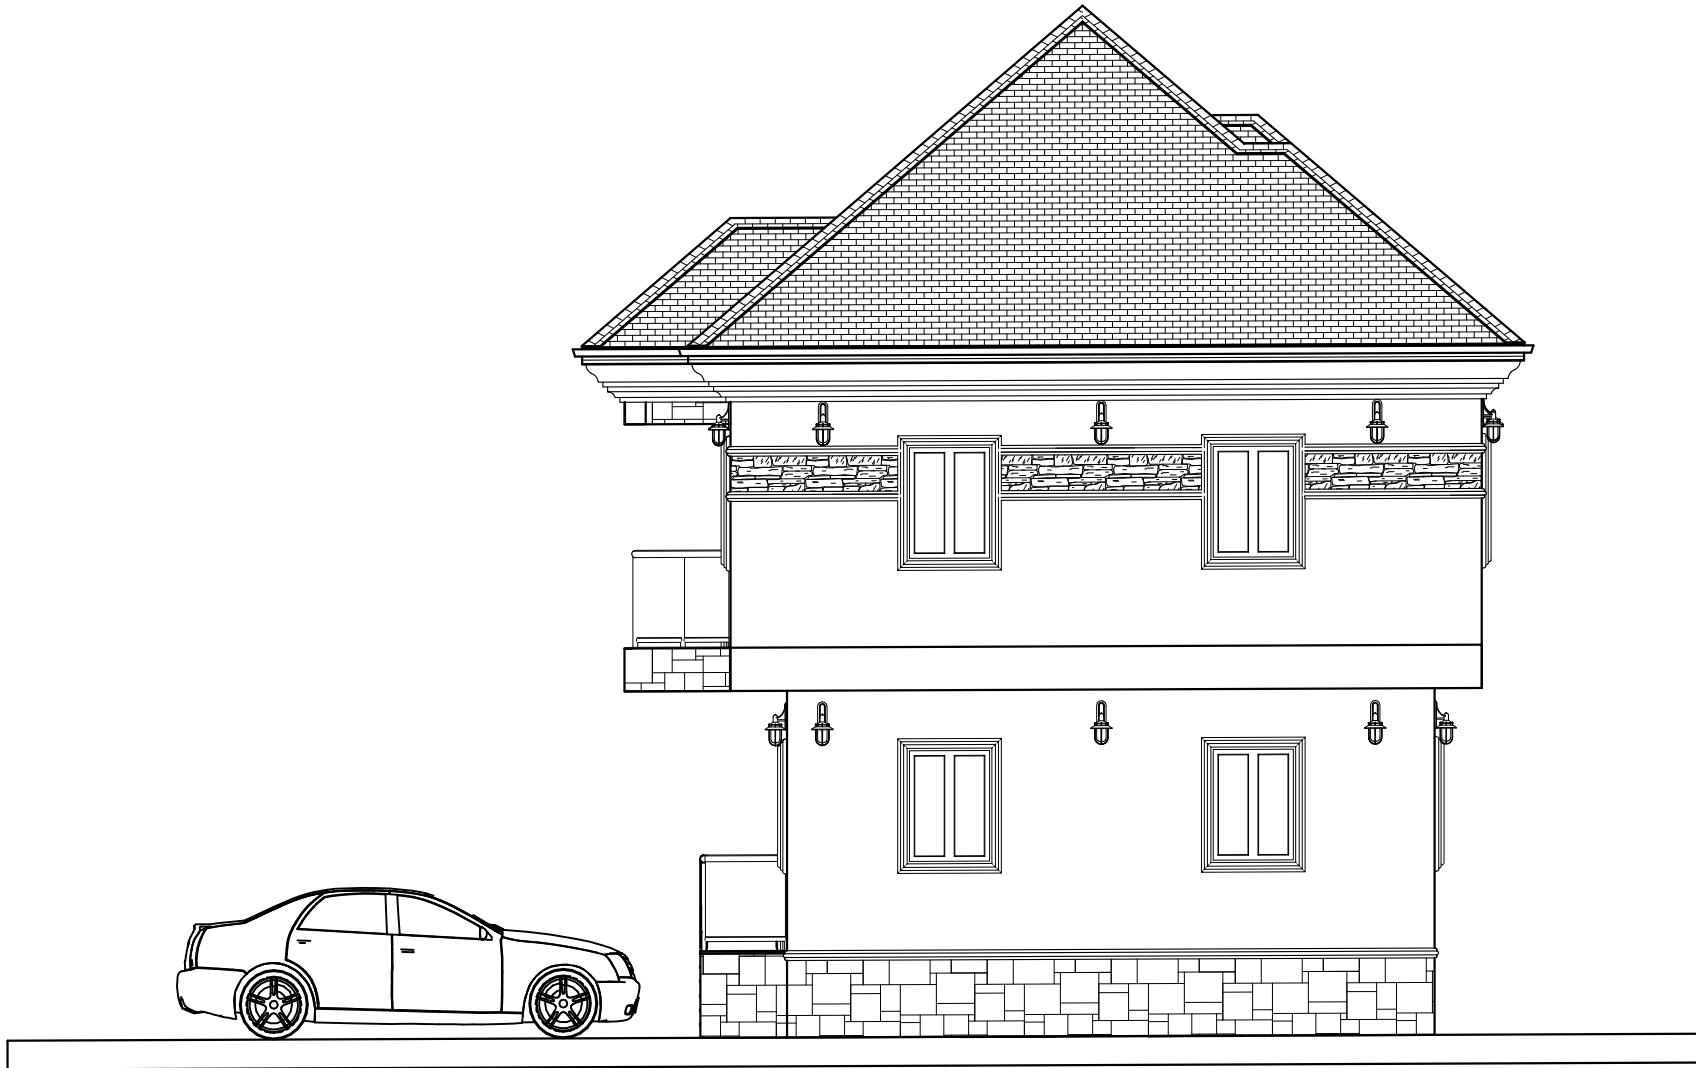

GENERAL NOTE.
1. Dimensions are to be read and not scaled.
2. All dimensions and conditions are to be verified on site before proceeding.
3. Drawings from all consultants relating to the same area should be read in conjunction with one another.
4. Should the contractor discern any conflicting information written or drawn, he is to notify the architect immediately.
5. This drawing is subject to world copyright and may not be reproduced in whole or in part for any purpose without prior written consent
Allcrownworks.

CLIENT.
MR OKUNOWO OMOLADE TOSIN.

PROJECT NAME AND ADDRESS.
PROPOSED RESIDENTIAL BUILDING PROJECT
@
22 SUNNY CLOSE,
DELE ADEDUGBE ESTATE,
FORMER WILLIAMS ELLIOT ESTATE,
NEW OKO-OBA,
IFAKO-IIAJYE LOCAL GOVT AREA,
LAGOS STATE.



DRAWING TITLE	REAR VIEW.
DATE	JANUARY 2024.
DESIGNED BY	ARCH TAYO CHARLES ADEDAPO. TEL: +2348033574252.
DRAWN BY	ALLCROWNWORKS. TEL: +2348071070888, +2348120156282.
CHECKED BY	ARCH TAYO CHARLES ADEDAPO.
SCALE	SCALE TO FIT.
SHEET A13	

GENERAL NOTE.

NO.	REVISION/ISSUE	DATE

EXISTING TWIN

ONE BEDROOM

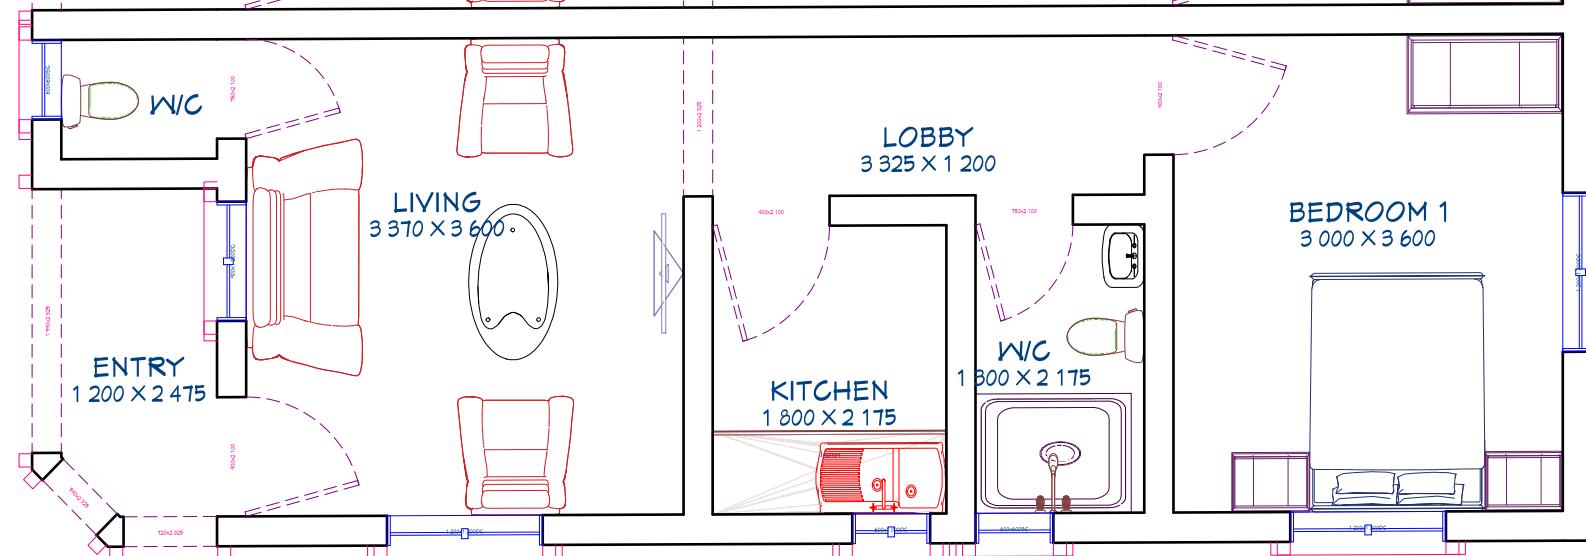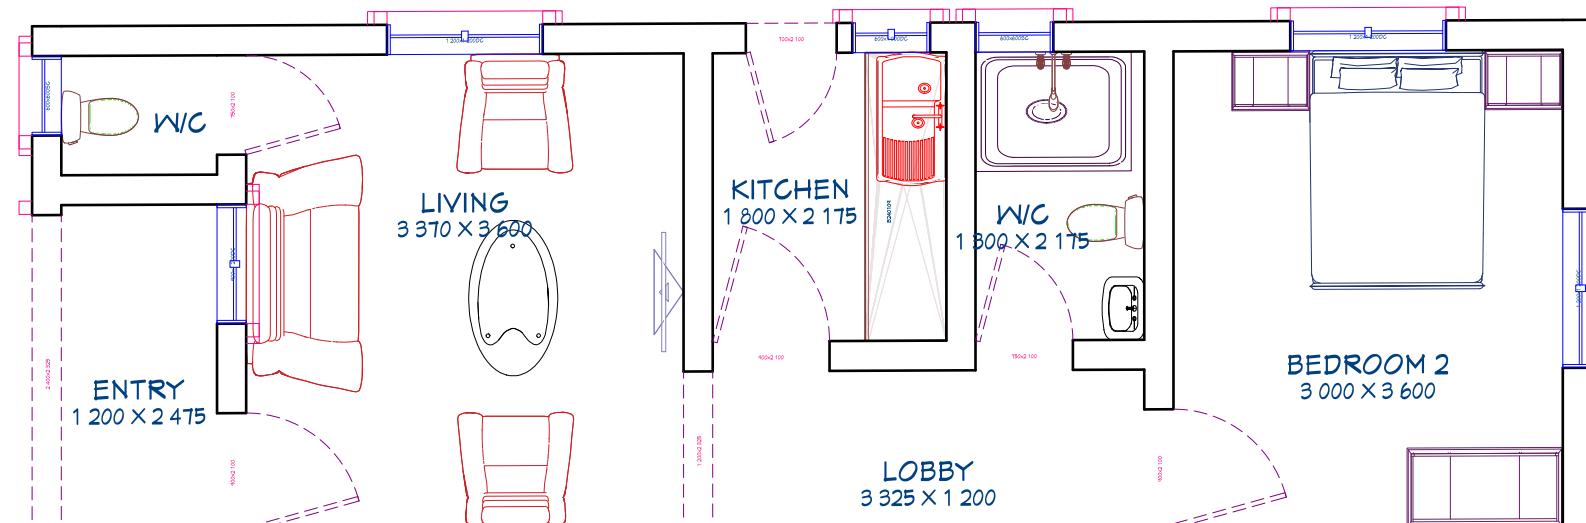

GENERAL NOTE.


- Dimensions are to be read and not scaled.
- All dimensions and conditions are to be verified on site before proceeding.
- Drawings from all consultants relating to the same area should be read in conjunction with one another.
- Should the contractor discern any conflicting information written or drawn, he is to notify the architect immediately.
- This drawing is subject to world copyright and may not be reproduced in whole or in part for any purpose without prior written consent Allcrownworks.

CLIENT.
MR OKUNOWO OMOLADE TOSIN.

PROJECT NAME AND ADDRESS.
PROPOSED RESIDENTIAL BUILDING PROJECT
@ 22 SUNNY CLOSE,
DELE ADEDUBU ESTATE,
FORMER WILLIAMS ELLIOT ESTATE,
NEW OKO-OBA,
IFAKO-IIAJYE LOCAL GOVT AREA,
LAGOS STATE.

DRAWING TITLE	FLOOR PLAN.
DATE	JANUARY 2024.
DESIGNED BY	ARCH TAYO CHARLES ADEDAPO. TEL: +2348033574252.
DRAWN BY	ALLCROWNWORKS. TEL: +2348071070888, +2348120156282.
CHECKED BY	ARCH TAYO CHARLES ADEDAPO.
SCALE	SCALE TO FIT.
SHEET	B1

GENERAL NOTE.
NO. REVISION/ISSUE DATE

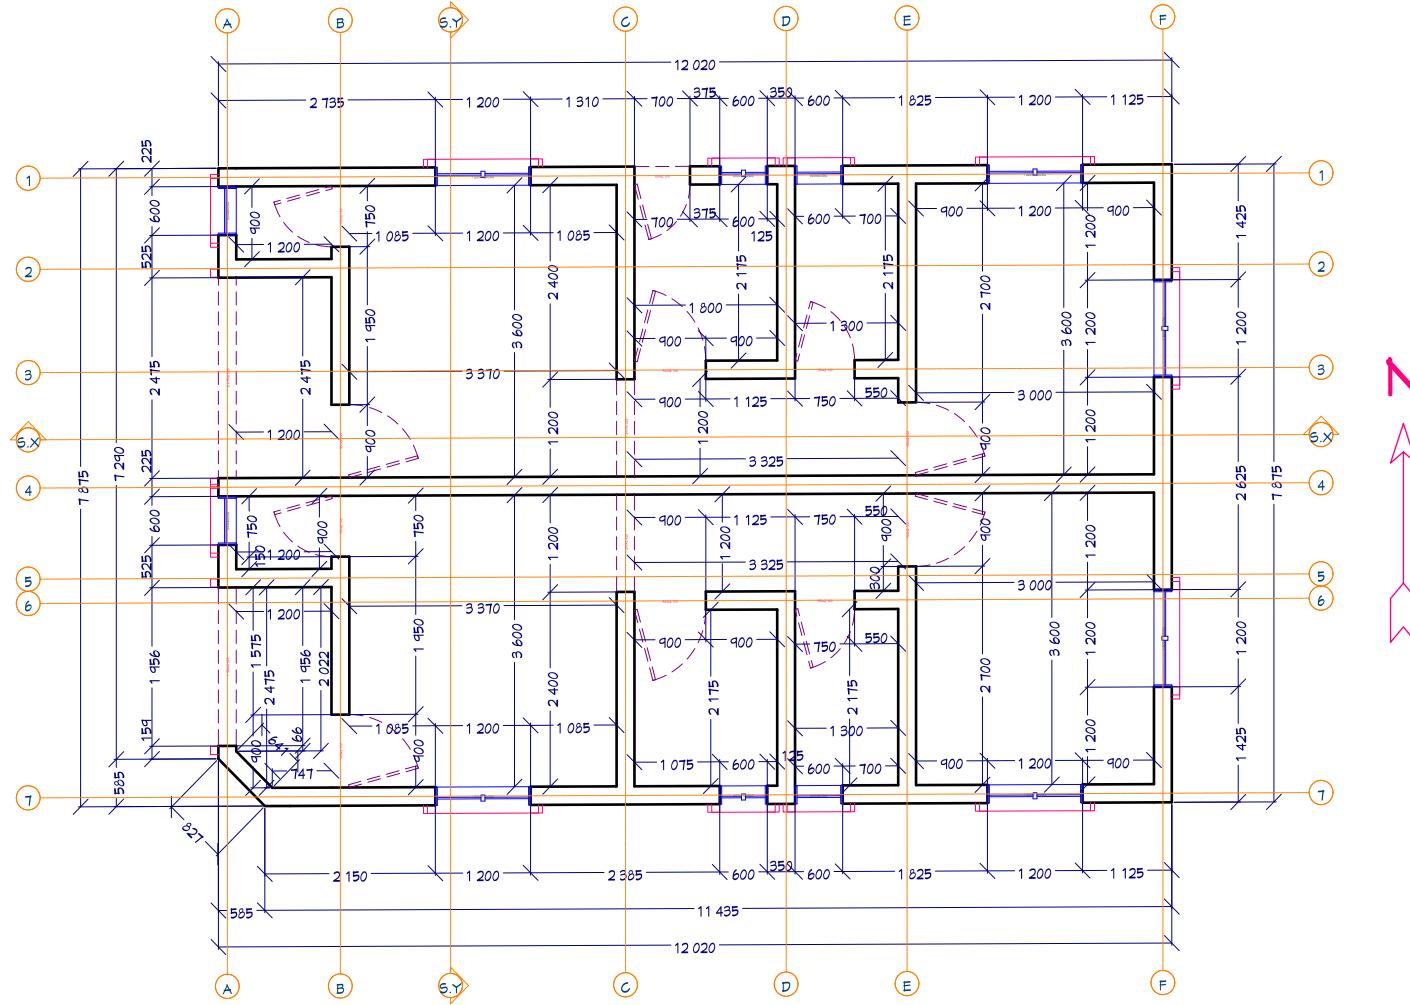

GENERAL NOTE:


1. Dimensions are to be read and not scaled.
2. All dimensions and conditions are to be verified on site before proceeding.
3. Drawings from all consultants relating to the same area should be read in conjunction with one another.
4. Should the contractor discern any conflicting information written or drawn, he is to notify the architect immediately.
5. This drawing is subject to world copyright and may not be reproduced in whole or in part for any purpose without prior written consent Allcrownworks.

CLIENT.
MR OKUNOWO OMOLADE TOSIN.

PROJECT NAME AND ADDRESS.
PROPOSED RESIDENTIAL BUILDING PROJECT
@ 22 SUNNY CLOSE,
DELE ADEDJUBE ESTATE,
FORMER WILLIAMS ELLIOT ESTATE,
NEW OKO-OBA,
IFAKO-IJAJE LOCAL GOVT AREA,
LAGOS STATE.

DRAWING TITLE	DIMENSION.	
DATE	JANUARY 2024.	
DESIGNED BY	ARCH TAYO CHARLES ADEDAPO.	TEL: +2348033574252.
DRAWN BY	ALLCROWNWORKS.	TEL: +2348071070888, +2348120156282.
CHECKED BY	ARCH TAYO CHARLES ADEDAPO.	
SCALE	SCALE TO FIT.	SHEET B2

GENERAL NOTE.
NO. REVISION/ISSUE DATE

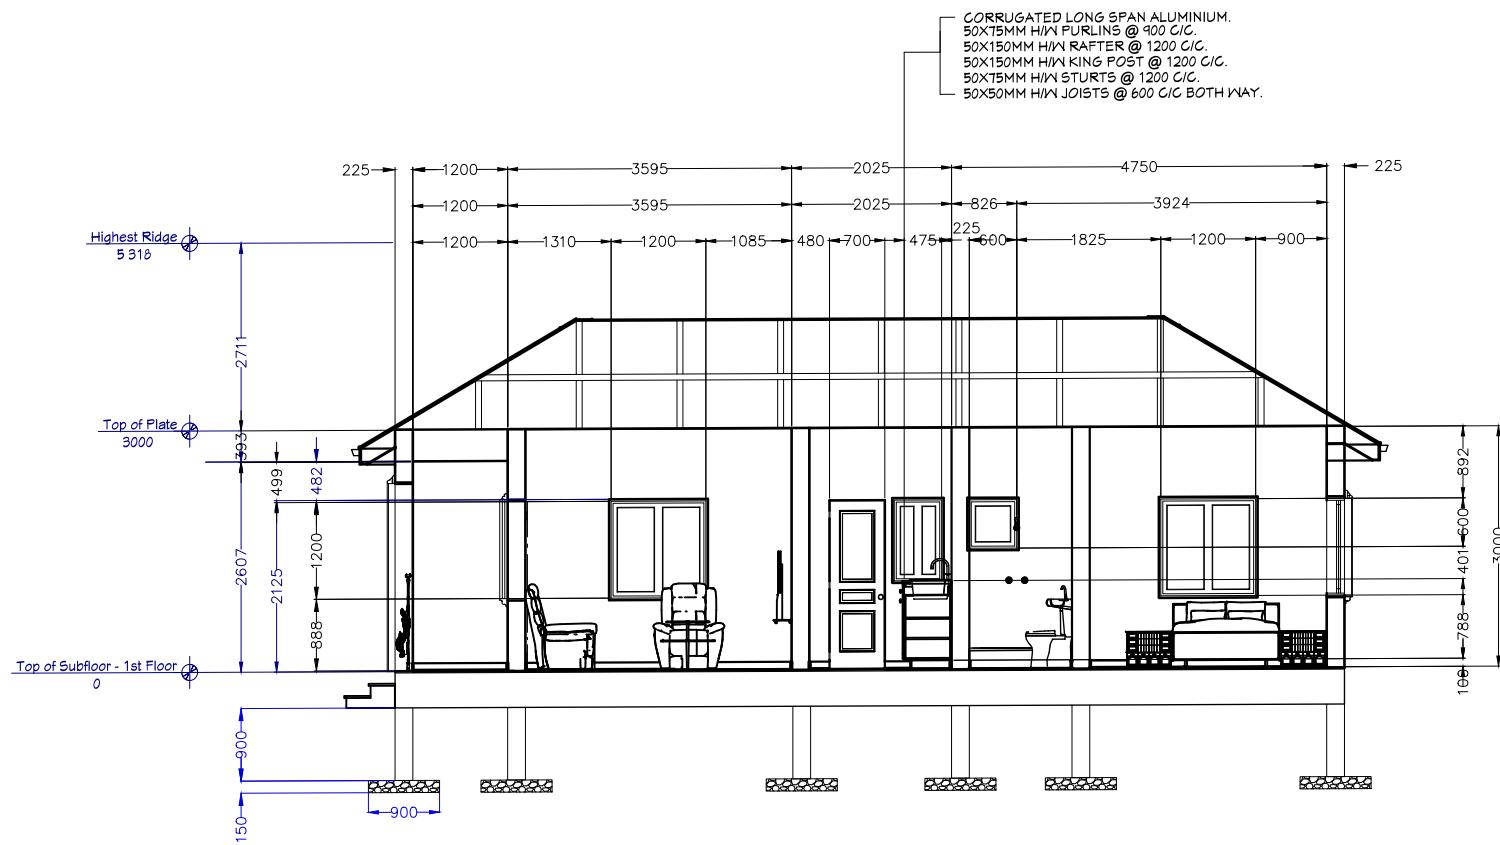

GENERAL NOTE.

1. Dimensions are to be read and not scaled.
2. All dimensions and conditions are to be verified on site before proceeding.
3. Drawings from all consultants relating to the same area should be read in conjunction with one another.
4. Should the contractor discern any conflicting information written or drawn, he is to notify the architect immediately.
5. This drawing is subject to world copyright and may not be reproduced in whole or in part for any purpose without prior written consent Allcrownworks.


CLIENT.
MR OKUNOWO OMOLADE TOSIN.

PROJECT NAME AND ADDRESS.
PROPOSED RESIDENTIAL BUILDING PROJECT
@ 22 SUNNY CLOSE,
DELE ADEDUGBE ESTATE,
FORMER WILLIAMS ELLIOT ESTATE,
NEW OKO-OBA,
IFAKO-IJAIYE LOCAL GOVT AREA,
LAGOS STATE.

DRAWING TITLE	SECTION Y.
DATE	JANUARY 2024.
DESIGNED BY	ARCH TAYO CHARLES ADEDAPO. TEL: +2348033574252.
DRAWN BY	ALLCROWNWORKS. TEL: +234807070888, +2348120156282.
CHECKED BY	ARCH TAYO CHARLES ADEDAPO.
SCALE	SCALE TO FIT.
SHEET B3	

GENERAL NOTE.

NO.	REVISION/ISSUE	DATE
-----	----------------	------

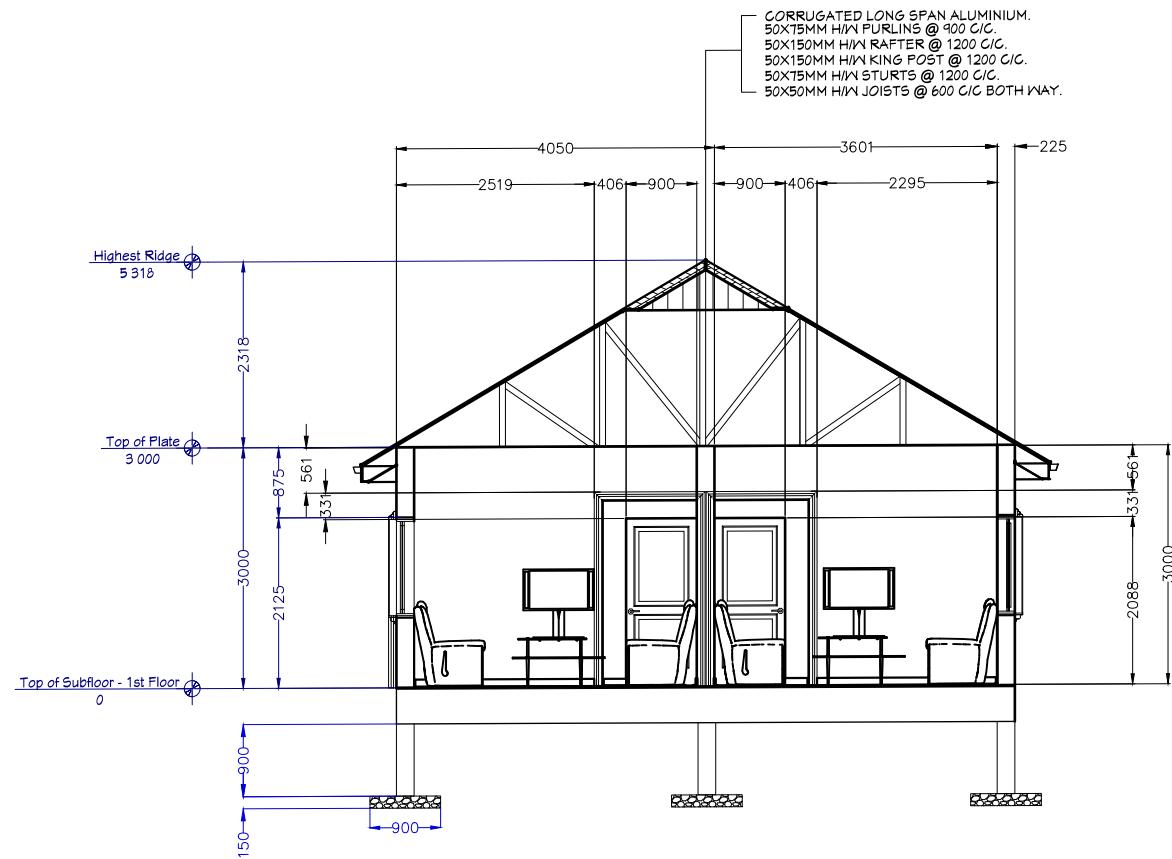

GENERAL NOTE:

1. Dimensions are to be read and not scaled.
2. All dimensions and conditions are to be verified on site before proceeding.
3. Drawings from all consultants relating to the same area should be read in conjunction with one another.
4. Should the contractor discern any conflicting information written or drawn, he is to notify the architect immediately.
5. This drawing is subject to world copyright and may not be reproduced in whole or in part for any purpose without prior written consent Allcrownworks.


CLIENT.
MR OKUNOWO OMOLADE TOSIN.

PROJECT NAME AND ADDRESS.
PROPOSED RESIDENTIAL BUILDING PROJECT
@
**22 SUNNY CLOSE,
DELE ADEDUBU ESTATE,
FORMER WILLIAMS ELLIOT ESTATE,
NEW OKO-OBA,
IFAKO-IJAYE LOCAL GOVT AREA,
LAGOS STATE.**

DRAWING TITLE	SECTION X.
DATE	JANUARY 2024.
DESIGNED BY	ARCH TAYO CHARLES ADEDAPO. TEL: +2348033574252.
DRAWN BY	ALLCROWNWORKS. TEL: +234807070888, +2348120156282.
CHECKED BY	ARCH TAYO CHARLES ADEDAPO.
SCALE	SCALE TO FIT.
	SHEET B4

GENERAL NOTE.

NO.	REVISION ISSUE	DATE

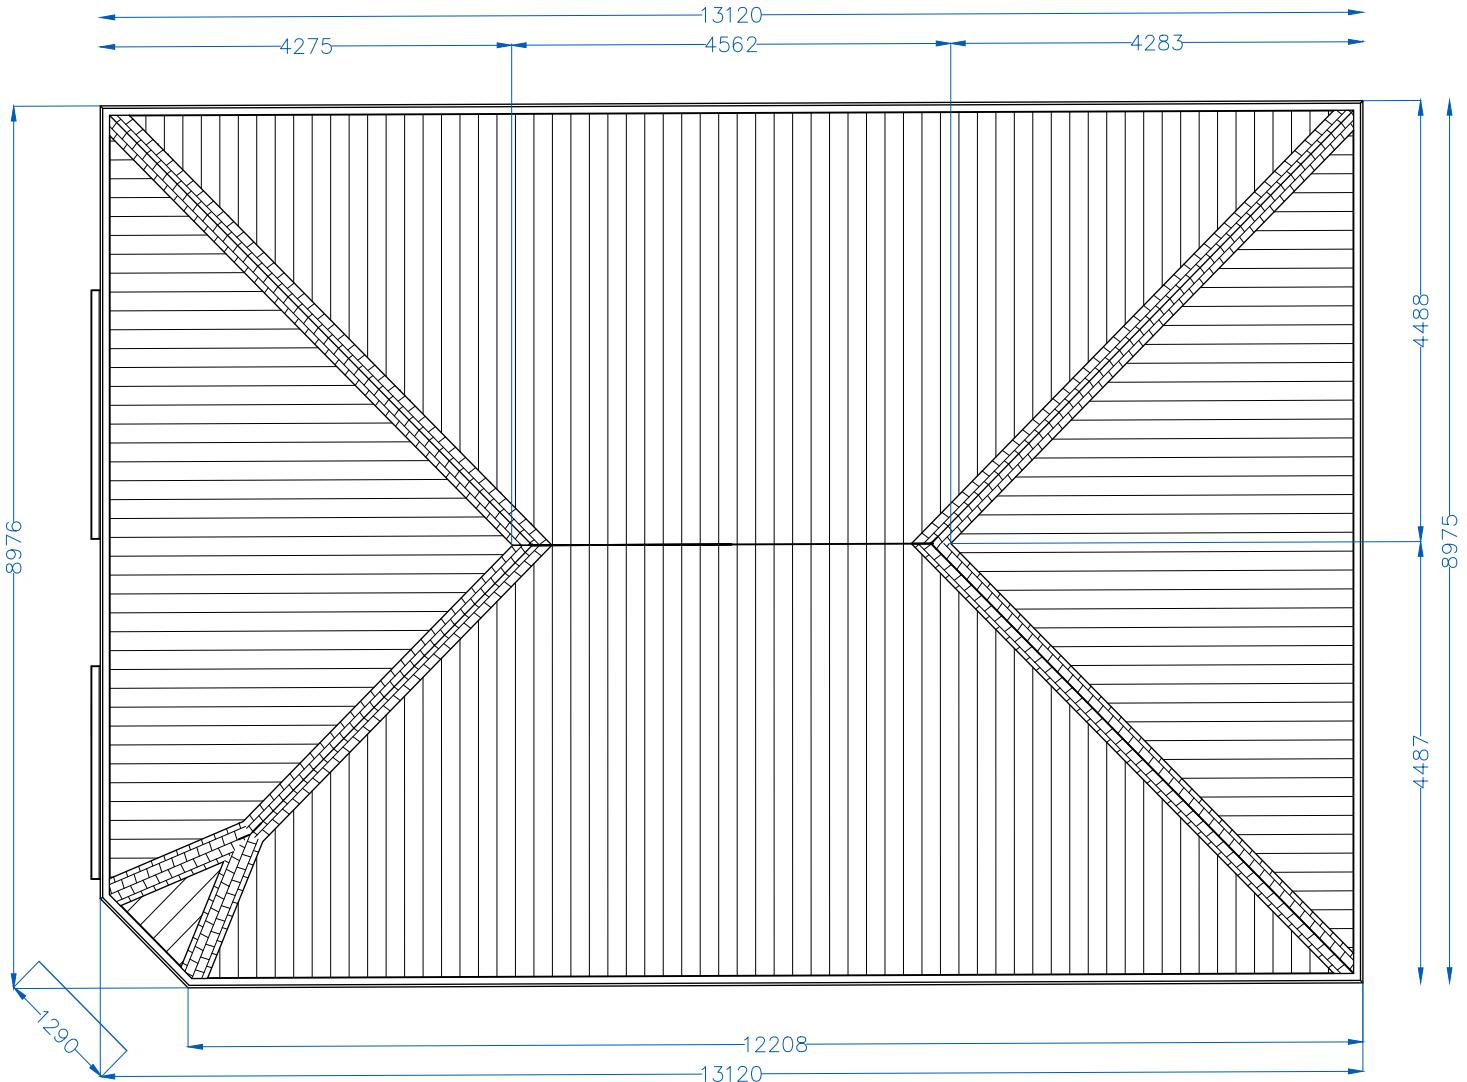

GENERAL NOTE.

- Dimensions are to be read and not scaled.
- All dimensions and conditions are to be verified on site before proceeding.
- Drawings from all consultants relating to the same area should be read in conjunction with one another.
- Should the contractor discern any conflicting information written or drawn, he is to notify the architect immediately.
- This drawing is subject to world copyright and may not be reproduced in whole or in part for any purpose without prior written consent Allcrownworks.

CLIENT.
MR OKUNOWO OMOLADE TOSIN.

PROJECT NAME AND ADDRESS.
PROPOSED RESIDENTIAL BUILDING PROJECT
@ 22 SUNNY CLOSE,
DELE ADEDUBU ESTATE,
FORMER WILLIAMS ELLIOT ESTATE,
NEW OKO-OBA,
IFAKO-IIAJYE LOCAL GOVT AREA,
LAGOS STATE.


DRAWING TITLE	ROOF.
DATE	JANUARY 2024.
DESIGNED BY	ARCH TAYO CHARLES ADEDAOPO. TEL: +2348033574252.
DRAWN BY	ALLCROWNWORKS. TEL: +2348071070888, +2348120156282.
CHECKED BY	ARCH TAYO CHARLES ADEDAOPO.
SCALE	SCALE TO FIT.
SHEET B5	

GENERAL NOTE.

NO.	REVISION/ISSUE	DATE



FRONT SIDE VIEW

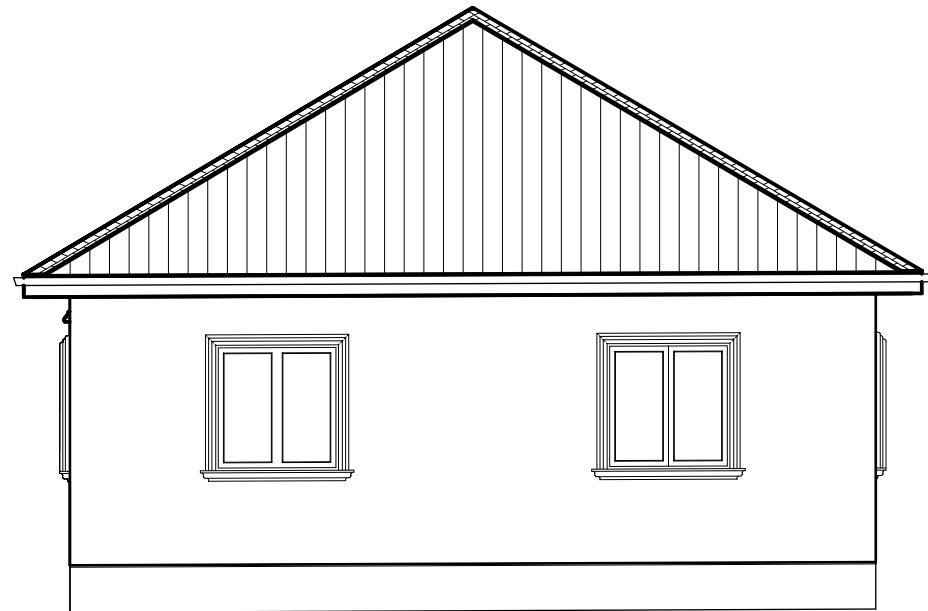

REAR VIEW

ARCHITECTURE FIRM NAME AND ADDRESS.
3A, ANIFOWOSHE STREET, ABULE EGBA IFAKO IJAYE, LAGOS

GENERAL NOTE.
1. Dimensions are to be read and not scaled.
2. All dimensions and conditions are to be verified on site before proceeding.
3. Drawings from all consultants relating to the same area should be read in conjunction with one another.
4. Should the contractor discern any conflicting information written or drawn, he is to notify the architect immediately.
5. This drawing is subject to world copyright and may not be reproduced in whole or in part for any purpose without prior written consent Allcrownworks.

CLIENT.
<u>MR OKUNOWO OMOLADE TOSIN.</u>


PROJECT NAME AND ADDRESS.
PROPOSED RESIDENTIAL BUILDING PROJECT @ 22 SUNNY CLOSE, DELE ADEDUGBE ESTATE, FORMER WILLIAMS ELLIOT ESTATE, NEW OKO-OBA, IFAKO-IJAYE LOCAL GOVT AREA, LAGOS STATE.

DRAWING TITLE	FRONT AND REAR VIEW.
DATE	JANUARY 2024.
DESIGNED BY	ARCH TAYO CHARLES ADEDAPO. TEL: +2348033574252.
DRAWN BY	ALLCROWNWORKS. TEL: +2348071070888, +2348120156282.
CHECKED BY	ARCH TAYO CHARLES ADEDAPO.
SCALE	SCALE TO FIT.
SHEET	B6

GENERAL NOTE.		
NO.	REVISION ISSUE	DATE



LEFT SIDE VIEW

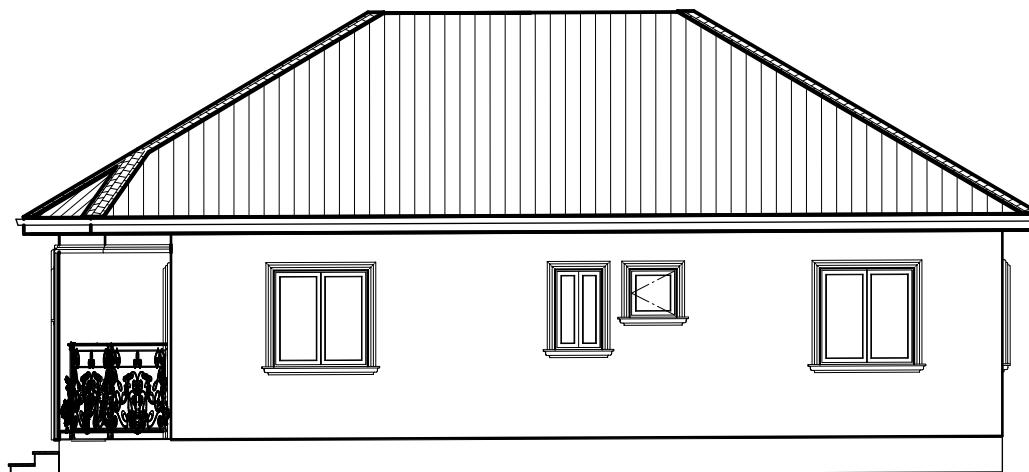

RIGHT SIDE VIEW



ARCHITECTURE FIRM NAME AND ADDRESS.

3A, ANIFOWOSHE STREET, ABULE EGBA IFAKO IIJAYE, LAGOS

GENERAL NOTE.
1. Dimensions are to be read and not scaled.
2. All dimensions and conditions are to be verified on site before proceeding.
3. Drawings from all consultants relating to the same area should be read in conjunction with one another.
4. Should the contractor discern any conflicting information written or drawn, he is to notify the architect immediately.
5. This drawing is subject to world copyright and may not be reproduced in whole or in part for any purpose without prior written consent Allcrownworks.

CLIENT.

MR OKUNOWO OMOLADE TOSIN.

PROJECT NAME AND ADDRESS.


PROPOSED RESIDENTIAL BUILDING PROJECT
@
22 SUNNY CLOSE,
DELE ADEDUGBE ESTATE,
FORMER WILLIAMS ELLIOT ESTATE,
NEW OKO-OBA,
IFAKO-IIAJYE LOCAL GOVT AREA,
LAGOS STATE.

DRAWING TITLE	RIGHT AND LEFT VIEW.
DATE	JANUARY 2024.
DESIGNED BY	ARCH TAYO CHARLES ADEDAPO. TEL: +2348033574252.
DRAWN BY	ALLCROWNWORKS. TEL: +2348071070888, +2348120156282.
CHECKED BY	ARCH TAYO CHARLES ADEDAPO.
SCALE	SCALE TO FIT.
	SHEET B7


GENERAL NOTE.		
NO.	REVISION ISSUE	DATE

EXISTING

3 BEDROOM

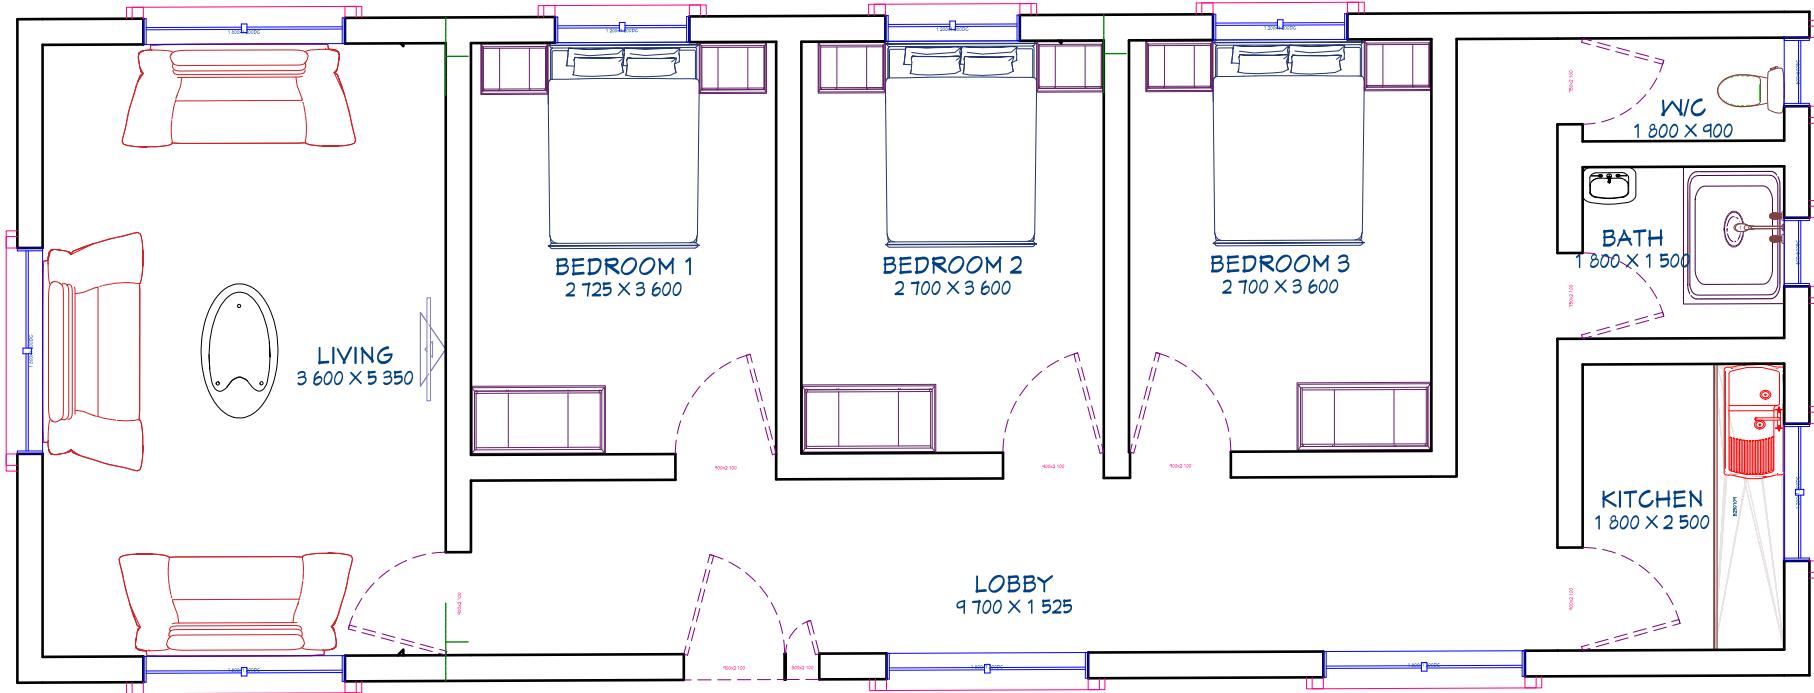

N

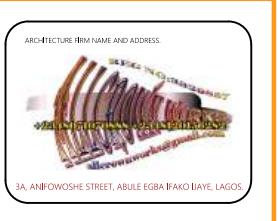

GENERAL NOTE.


- Dimensions are to be read and not scaled.
- All dimensions and conditions are to be verified on site before proceeding.
- Drawings from all consultants relating to the same area should be read in conjunction with one another.
- Should the contractor discern any conflicting information written or drawn, he is to notify the architect immediately.
- This drawing is subject to world copyright and may not be reproduced in whole or in part for any purpose without prior written consent Allcrownworks.

CLIENT.
MR OKUNOWO OMOLADE TOSIN.

PROJECT NAME AND ADDRESS.
PROPOSED RESIDENTIAL BUILDING PROJECT
@ 22 SUNNY CLOSE,
DELE ADEDUGBE ESTATE,
FORMER WILLIAMS ELLIOT ESTATE,
NEW OKO-OBA,
IFAKO-IIAJA LOCAL GOVT AREA,
LAGOS STATE.

DRAWING TITLE	FLOOR PLAN.
DATE	JANUARY 2024.
DESIGNED BY	ARCH TAYO CHARLES ADEDAPO. TEL: +2348033574252.
DRAWN BY	ALLCROWNWORKS. TEL: +2348071070888, +2348120156282.
CHECKED BY	ARCH TAYO CHARLES ADEDAPO.
SCALE	SCALE TO FIT.
SHEET C1	

GENERAL NOTE.		
NO.	REVISION ISSUE	DATE

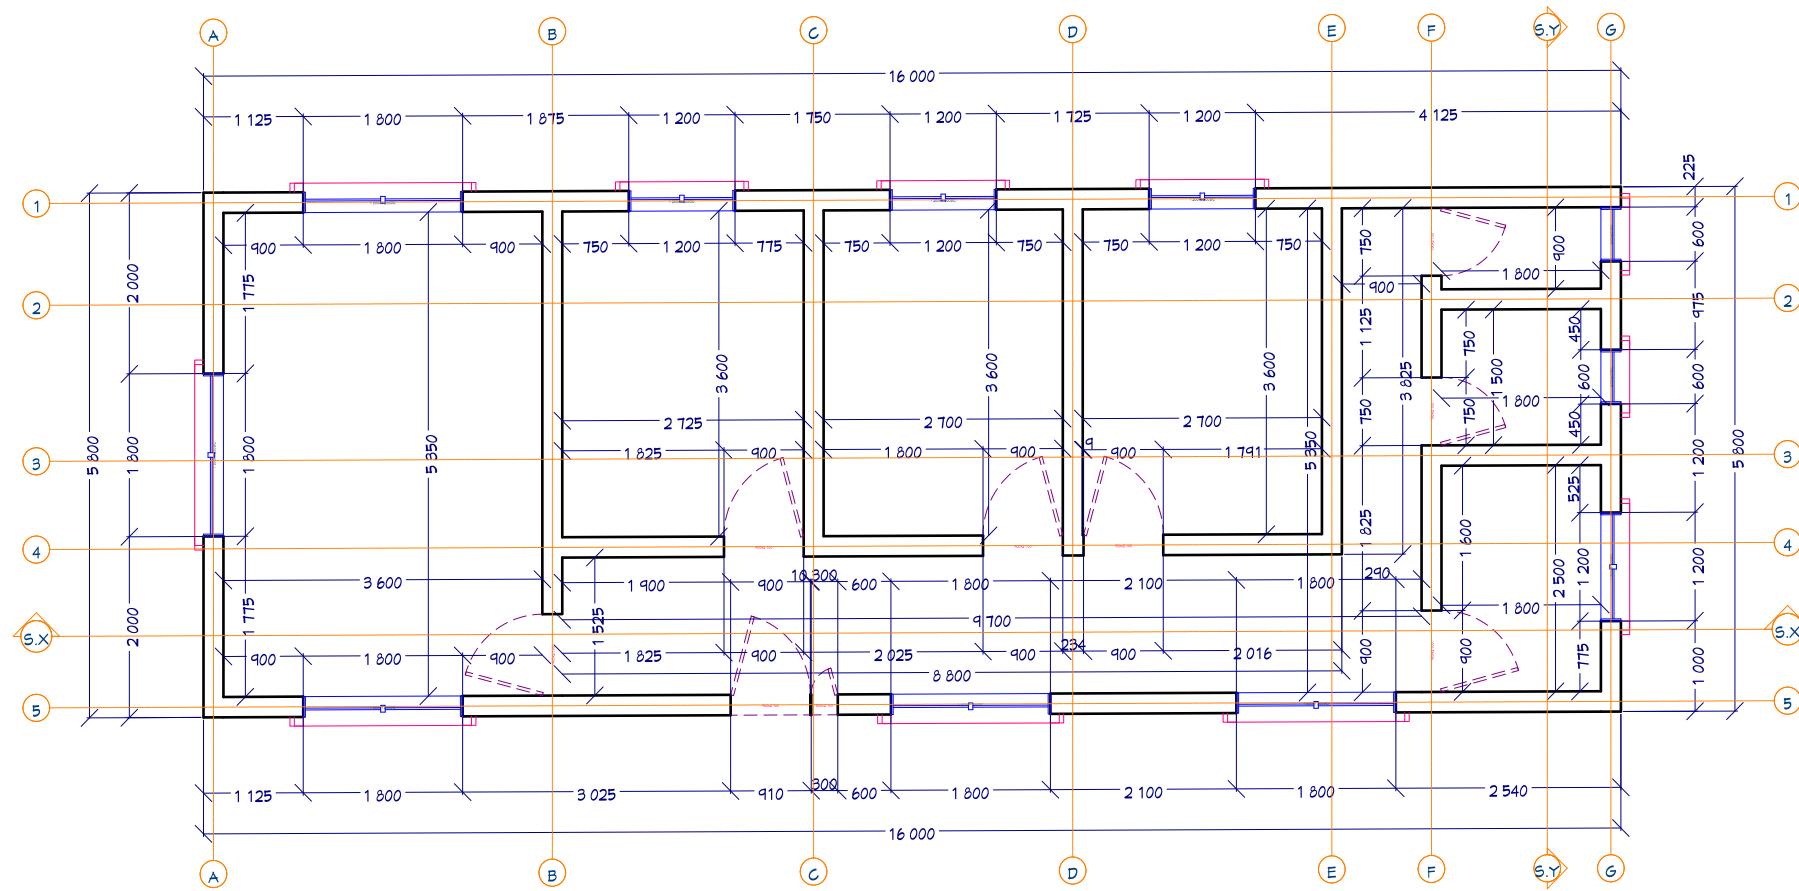

GENERAL NOTE.


- Dimensions are to be read and not scaled.
- All dimensions and conditions are to be verified on site before proceeding.
- Drawings from all consultants relating to the same area should be read in conjunction with one another.
- Should the contractor discern any conflicting information written or drawn, he is to notify the architect immediately.
- This drawing is subject to world copyright and may not be reproduced in whole or in part for any purpose without prior written consent Allcrownworks.

CLIENT.
MR OKUNOWO OMOLADE TOSIN.

PROJECT NAME AND ADDRESS.
PROPOSED RESIDENTIAL BUILDING PROJECT
@ 22 SUNNY CLOSE,
DELE ADEDUGBE ESTATE,
FORMER WILLIAMS ELLIOT ESTATE,
NEW OKO-OBA,
IFAKO-IJAIYE LOCAL GOVT AREA,
LAGOS STATE.

DRAWING TITLE	DIMENSION.
DATE	JANUARY 2024.
DESIGNED BY	ARCH TAYO CHARLES ADEDAPO. TEL: +2348033574252.
DRAWN BY	ALLCROWNWORKS. TEL: +234807070888, +2348120156282.
CHECKED BY	ARCH TAYO CHARLES ADEDAPO.
SCALE	SCALE TO FIT.
	SHEET C2

GENERAL NOTE.		
NO.	REVISION/ISSUE	DATE

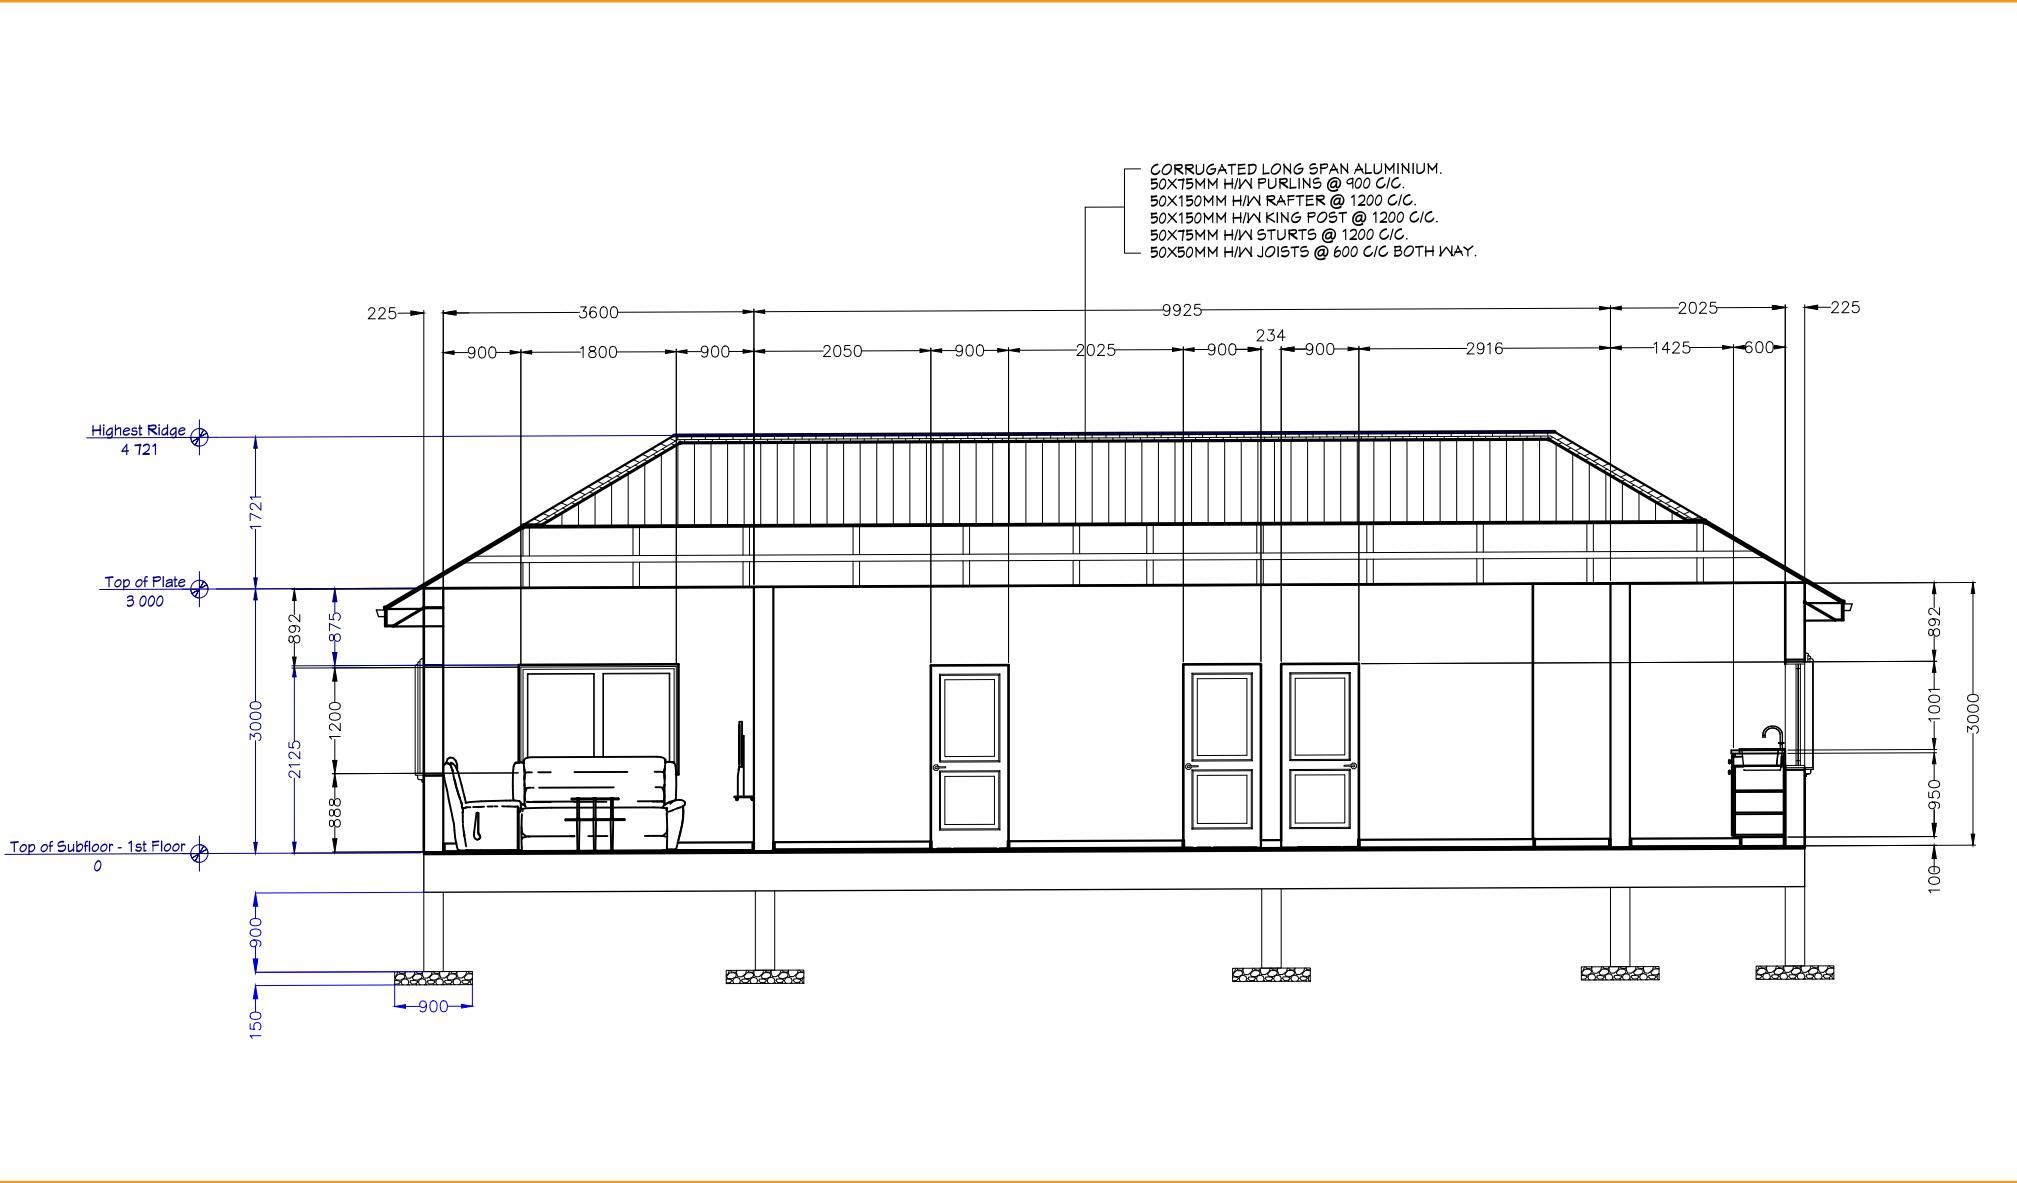

GENERAL NOTE.

1. Dimensions are to be read and not scaled.
2. All dimensions and conditions are to be verified on site before proceeding.
3. Drawings from all consultants relating to the same area should be read in conjunction with one another.
4. Should the contractor discern any conflicting information written or drawn, he is to notify the architect immediately.
5. This drawing is subject to world copyright and may not be reproduced in whole or in part for any purpose without prior written consent Allcrownworks.


CLIENT.
MR OKUNOWO OMOLADE TOSIN.

PROJECT NAME AND ADDRESS.
PROPOSED RESIDENTIAL BUILDING PROJECT
 @ 22 SUNNY CLOSE,
 DELE ADEDUBU ESTATE,
 FORMER WILLIAMS ELLIOT ESTATE,
 NEW OKO-OBA,
 IFAKO-IIAJYE LOCAL GOVT AREA,
 LAGOS STATE.

DRAWING TITLE	SECTION X.
DATE	JANUARY 2024.
DESIGNED BY	ARCH TAYO CHARLES ADEDAOPO. TEL: +2348033574252.
DRAWN BY	ALLCROWNWORKS. TEL: +2348071070888, +2348120156282.
CHECKED BY	ARCH TAYO CHARLES ADEDAOPO.
SCALE	SCALE TO FIT.
SHEET C3	

GENERAL NOTE.

NO.	REVISION ISSUE	DATE
-----	----------------	------

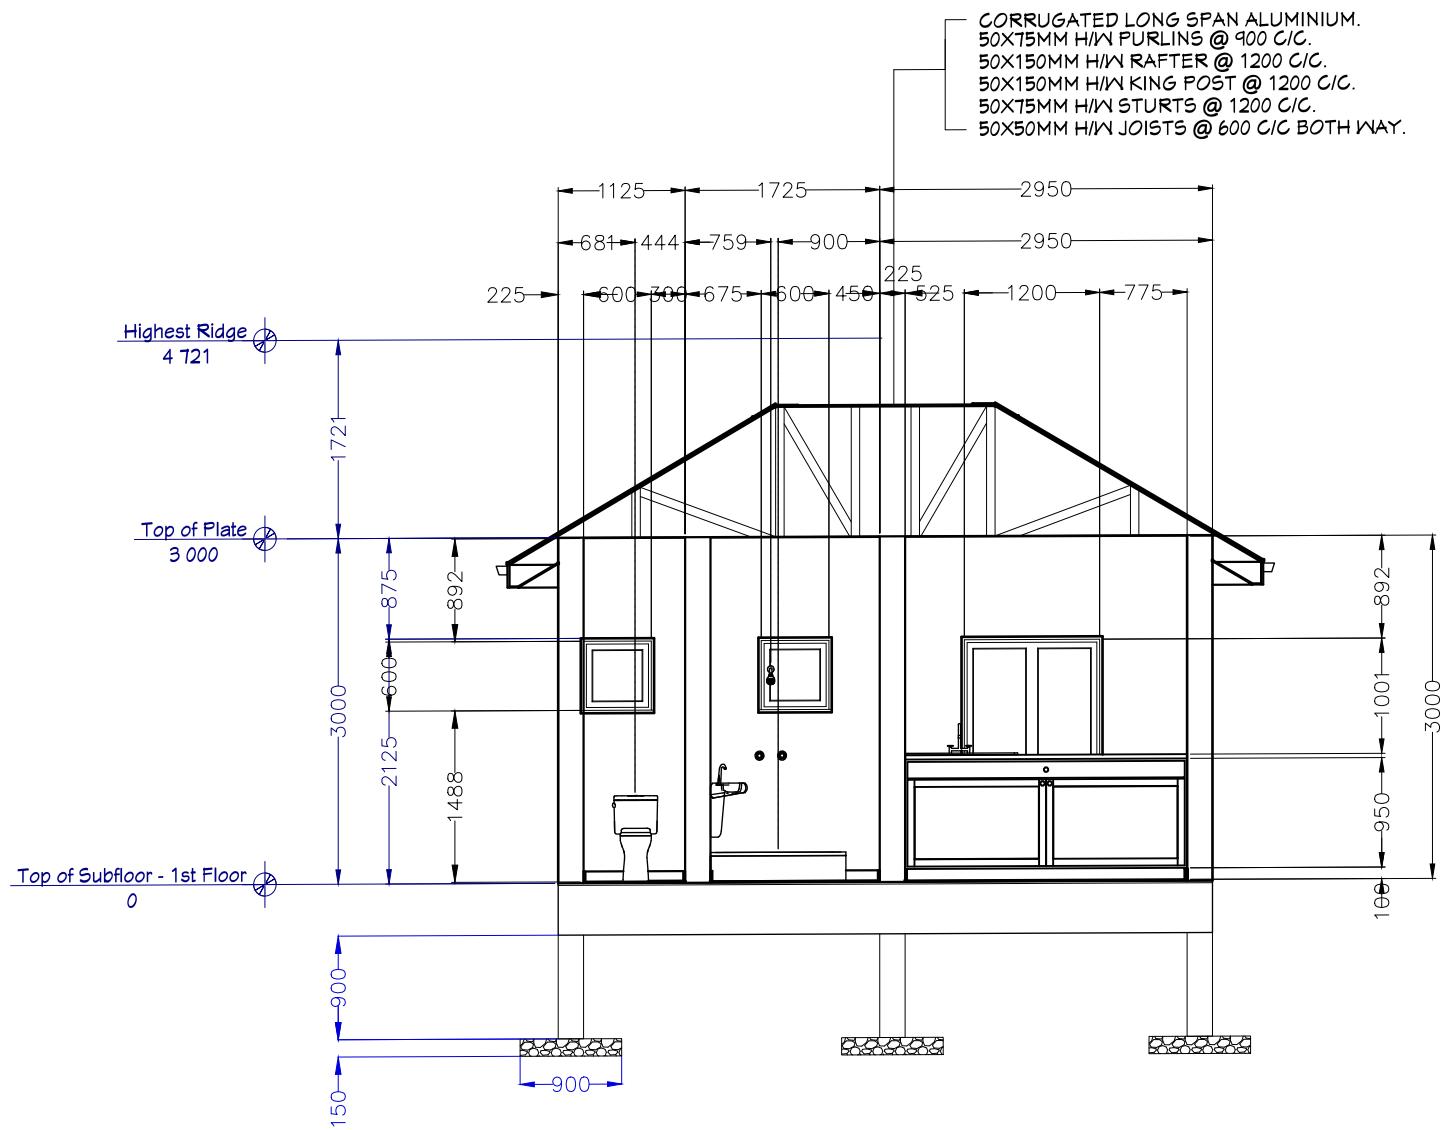

GENERAL NOTE.
 1. Dimensions are to be read and not scaled.
 2. All dimensions and conditions are to be verified on site before proceeding.
 3. Drawings from all consultants relating to the same area should be read in conjunction with one another.
 4. Should the contractor discern any conflicting information written or drawn, he is to notify the architect immediately.
 5. This drawing is subject to world copyright and may not be reproduced in whole or in part for any purpose without prior written consent Allcrownworks.


CLIENT.
MR OKUNOWO OMOLADE TOSIN.

PROJECT NAME AND ADDRESS.
PROPOSED RESIDENTIAL BUILDING PROJECT
 @ 22 SUNNY CLOSE,
 DELE ADEDUGBE ESTATE,
 FORMER WILLIAMS ELLIOT ESTATE,
 NEW OKO-OBA,
 IFAKO-IIAJYE LOCAL GOVT AREA,
 LAGOS STATE.

DRAWING TITLE	SECTION X.
DATE	JANUARY 2024.
DESIGNED BY	ARCH TAYO CHARLES ADEDAO. TEL: +2348033574252.
DRAWN BY	ALLCROWNWORKS. TEL: +234807070888, +2348120156282.
CHECKED BY	ARCH TAYO CHARLES ADEDAO.
SCALE	SCALE TO FIT.
SHEET C3	

GENERAL NOTE.

NO.	REVISION ISSUE	DATE

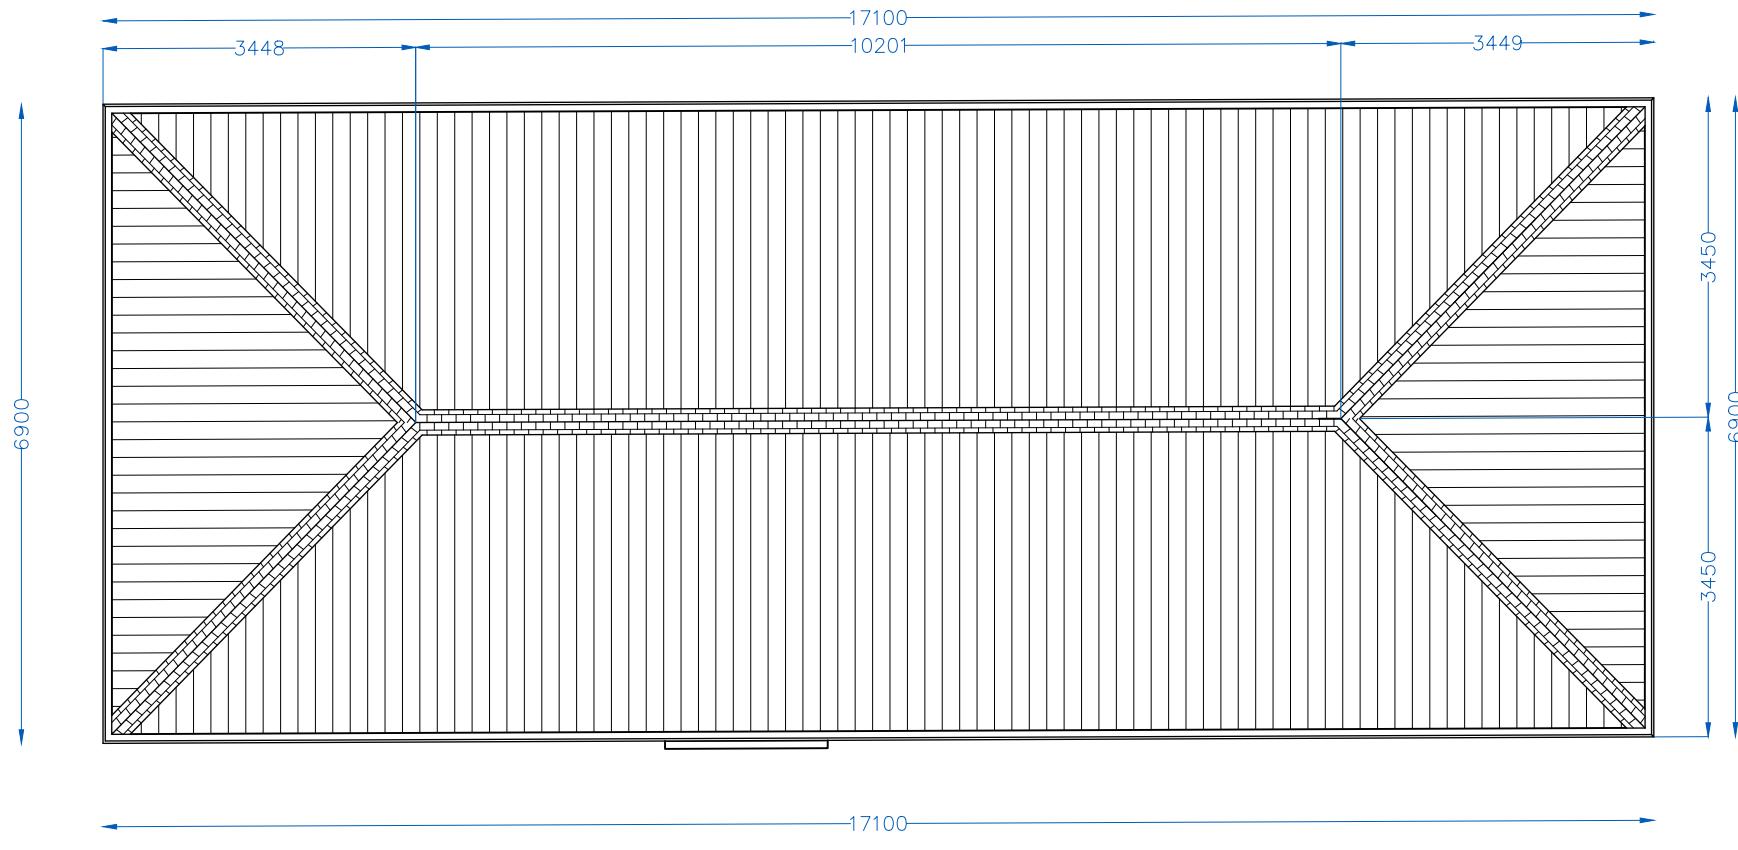

GENERAL NOTE.

- Dimensions are to be read and not scaled.
- All dimensions and conditions are to be verified on site before proceeding.
- Drawings from all consultants relating to the same area should be read in conjunction with one another.
- Should the contractor discern any conflicting information written or drawn, he is to notify the architect immediately.
- This drawing is subject to world copyright and may not be reproduced in whole or in part for any purpose without prior written consent Allcrownworks.

CLIENT.

MR OKUNOWO OMOLADE TOSIN.

PROJECT NAME AND ADDRESS.


PROPOSED RESIDENTIAL BUILDING PROJECT

© 22 SUNNY CLOSE,
DELE ADEDUGBE ESTATE,
FORMER WILLIAMS ELLIOT ESTATE,
NEW OKO-OBA,
IFAKO-IIAJYE LOCAL GOVT AREA,
LAGOS STATE.


DRAWING TITLE	ROOF.
DATE	JANUARY 2024.
DESIGNED BY	ARCH TAYO CHARLES ADEDAPO. TEL: +2348033574252.
DRAWN BY	ALLCROWNWORKS. TEL: +2348071070888, +2348120156282.
CHECKED BY	ARCH TAYO CHARLES ADEDAPO.
SCALE	SCALE TO FIT.
SHEET C5	

GENERAL NOTE.

NO.	REVISION/ISSUE	DATE

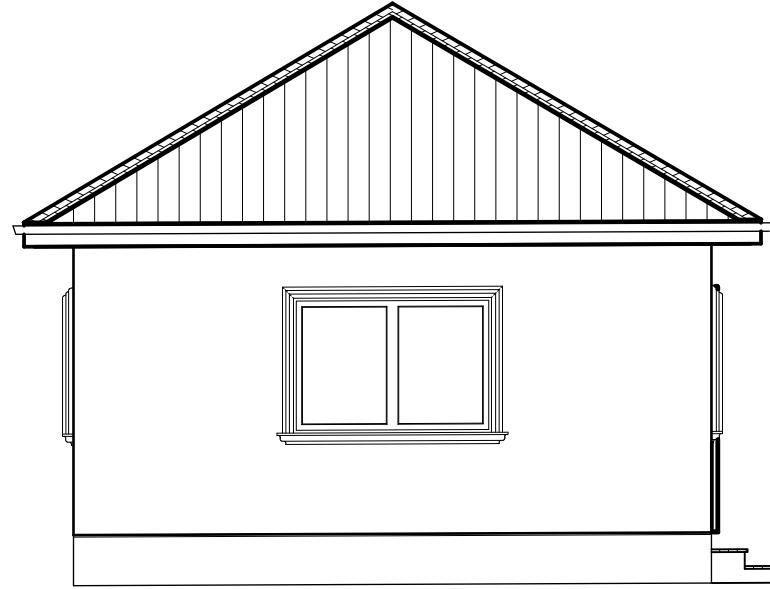

LEFT SIDE VIEW

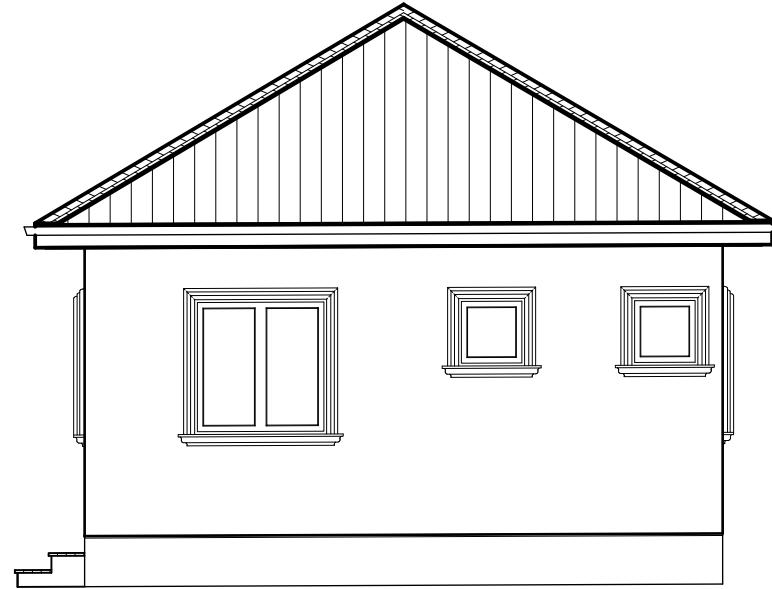


RIGHT SIDE VIEW




ARCHITECTURE FIRM NAME AND ADDRESS.

3A, ANIFOWOSHE STREET, ABULE EGBA IFAKO IJAYE, LAGOS

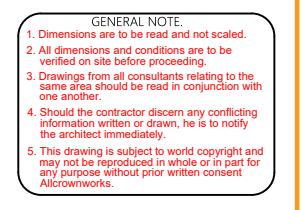

GENERAL NOTE:

1. Dimensions are to be read and not scaled.
2. All dimensions and conditions are to be verified on site before proceeding.
3. Drawings from all consultants relating to the same area should be read in conjunction with one another.
4. Should the contractor discern any conflicting information written or drawn, he is to notify the architect immediately.
5. This drawing is subject to world copyright and may not be reproduced in whole or in part for any purpose without prior written consent Allcrownworks.

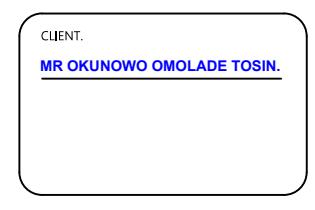


CLIENT.

MR OKUNOWO OMOLADE TOSIN.



PROJECT NAME AND ADDRESS.

PROPOSED RESIDENTIAL BUILDING PROJECT
@
22 SUNNY CLOSE,
DELE ADEDUGBE ESTATE,
FORMER WILLIAMS ELLIOT ESTATE,
NEW OKO-OBA,
IFAKO-IJAYE LOCAL GOVT AREA,
LAGOS STATE.

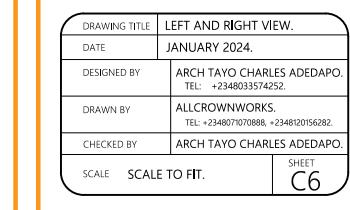

DRAWING TITLE

LEFT AND RIGHT VIEW.

DATE

JANUARY 2024.

DESIGNED BY

ARCH TAYO CHARLES ADEDAPO.
TEL: +2348033574252.

DRAWN BY

ALLCROWNWORKS.
TEL: +2348071070888, +2348120156282.

CHECKED BY


ARCH TAYO CHARLES ADEDAPO.

SCALE

SCALE TO FIT.

SHEET

C6

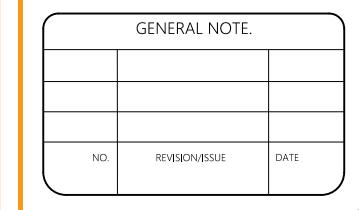


GENERAL NOTE.


NO.

REVISION/ISSUE

DATE

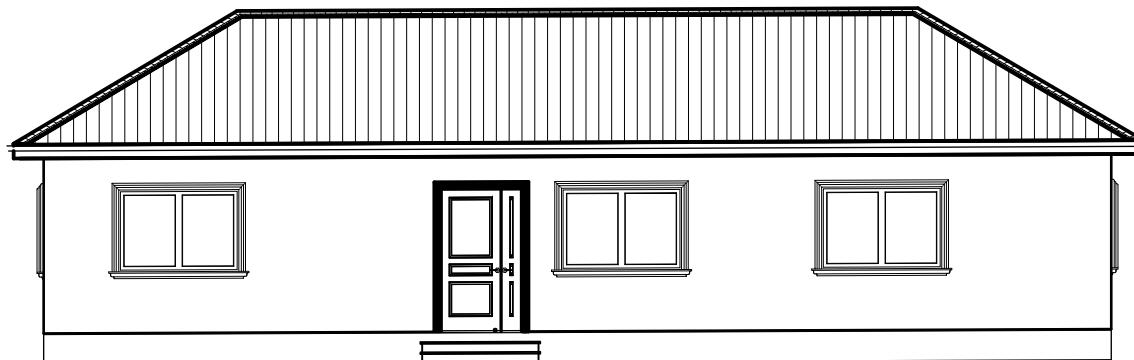

FRONT SIDE VIEW

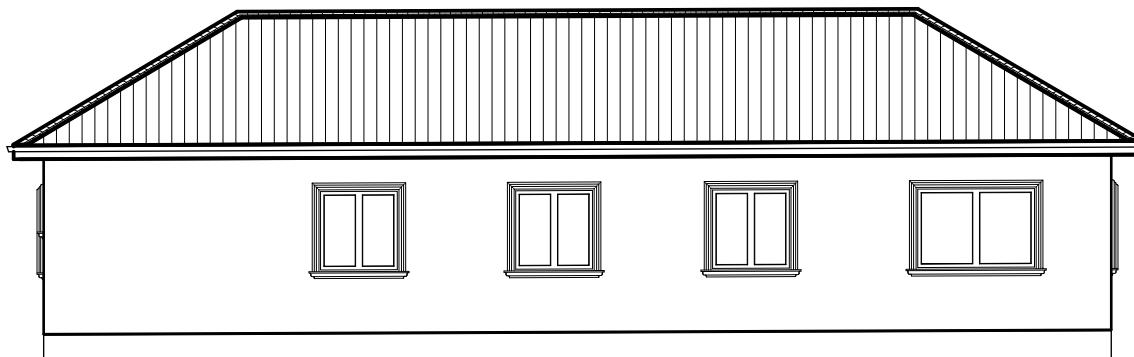

REAR VIEW



ARCHITECTURE FIRM NAME AND ADDRESS.

3A, ANIFOWOSHE STREET, ABULE EGBA IFAKO IIAYE, LAGOS

GENERAL NOTE.
1. Dimensions are to be read and not scaled.
2. All dimensions and conditions are to be verified on site before proceeding.
3. Drawings from all consultants relating to the same area should be read in conjunction with one another.
4. Should the contractor discern any conflicting information written or drawn, he is to notify the architect immediately.
5. This drawing is subject to world copyright and may not be reproduced in whole or in part for any purpose without prior written consent Allcrownworks.

CLIENT.
MR OKUNOWO OMOLADE TOSIN.

PROJECT NAME AND ADDRESS.
PROPOSED RESIDENTIAL BUILDING PROJECT
@
22 SUNNY CLOSE,
DELE ADEDUGBE ESTATE,
FORMER WILLIAMS ELLIOT ESTATE,
NEW OKO-OBA,
IFAKO-IIAJYE LOCAL GOVT AREA,
LAGOS STATE.


DRAWING TITLE	FRONT AND REAR VIEW.	
DATE	JANUARY 2024.	
DESIGNED BY	ARCH TAYO CHARLES ADEDAPO.	TEL: +2348033574252.
DRAWN BY	ALLCROWNWORKS.	TEL: +2348071070888, +2348120156282.
CHECKED BY	ARCH TAYO CHARLES ADEDAPO.	
SCALE	SCALE TO FIT.	SHEET C7

GENERAL NOTE.

NO.	REVISION ISSUE	DATE

SECURITY

HOUSE

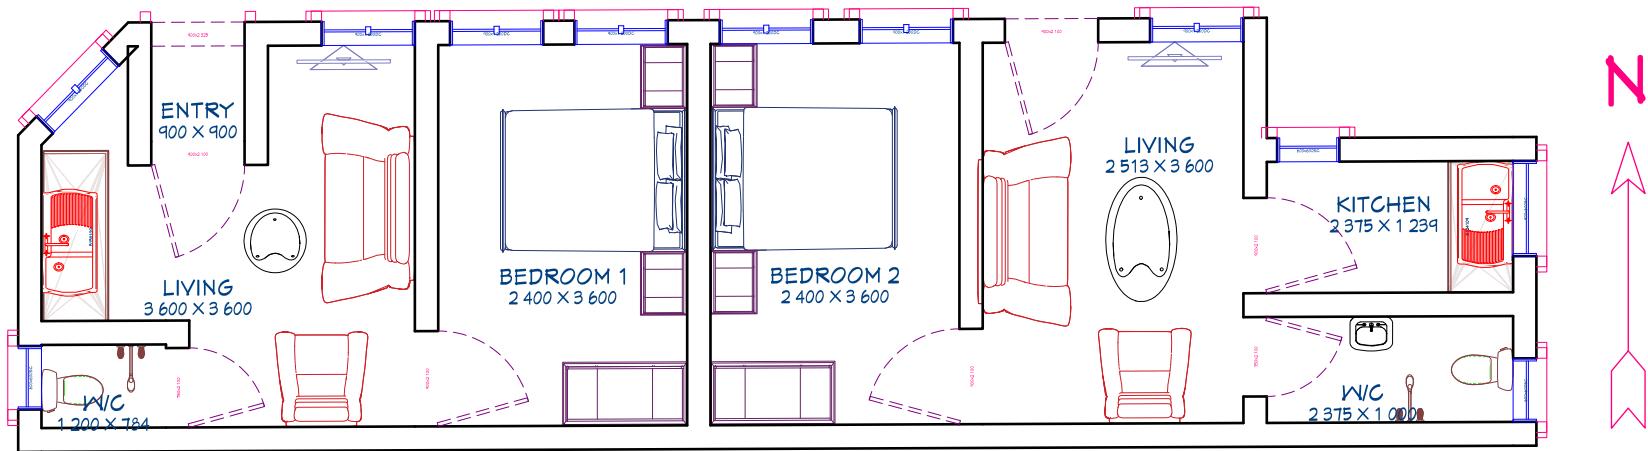

GENERAL NOTE:

1. Dimensions are to be read and not scaled.
2. All dimensions and conditions are to be verified on site before proceeding.
3. Drawings from all consultants relating to the same area should be read in conjunction with one another.
4. Should the contractor discern any conflicting information written or drawn, he is to notify the architect immediately.
5. This drawing is subject to world copyright and may not be reproduced in whole or in part for any purpose without prior written consent Allcrownworks.


CLIENT.
MR OKUNOWO OMOLADE TOSIN.

PROJECT NAME AND ADDRESS.
PROPOSED RESIDENTIAL BUILDING PROJECT
@ 22 SUNNY CLOSE,
DELE ADEDUGBE ESTATE,
FORMER WILLIAMS ELLIOT ESTATE,
NEW OKO-OBA,
IFAKO-IJAYE LOCAL GOVT AREA,
LAGOS STATE.

DRAWING TITLE	FLOOR PLAN.
DATE	JANUARY 2024.
DESIGNED BY	ARCH TAYO CHARLES ADEDAPO. TEL: +2348033574252.
DRAWN BY	ALLCROWNWORKS. TEL: +2348071070888, +2348120156282.
CHECKED BY	ARCH TAYO CHARLES ADEDAPO.
SCALE	SCALE TO FIT.
SHEET D1	

GENERAL NOTE.

NO.	REVISION ISSUE	DATE

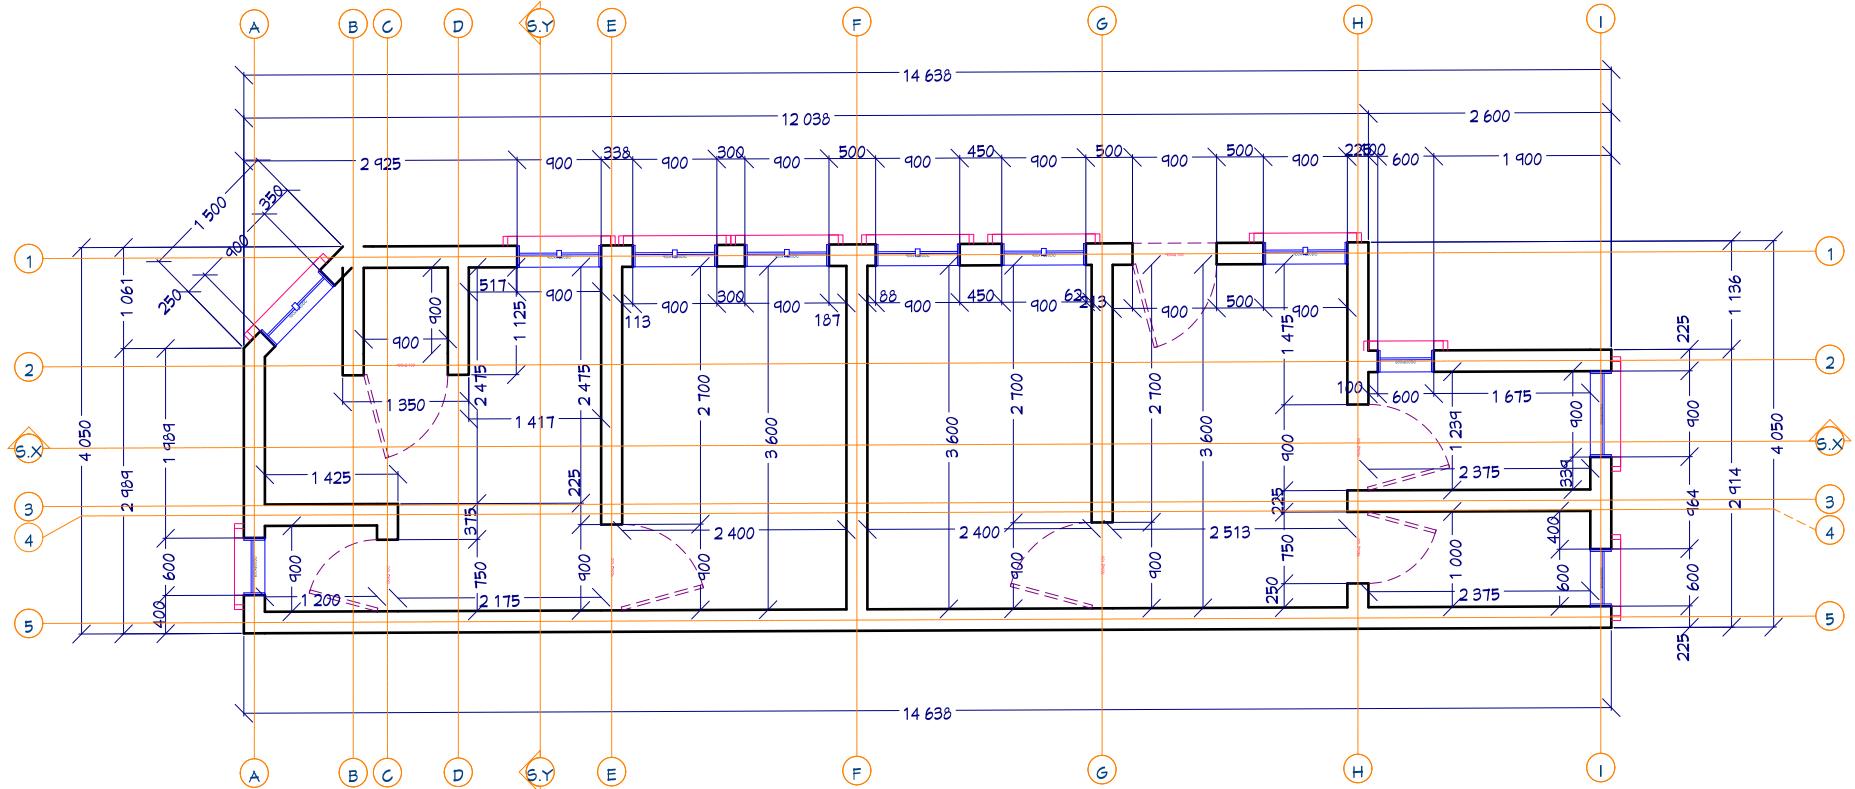

GENERAL NOTE.


- Dimensions are to be read and not scaled.
- All dimensions and conditions are to be verified on site before proceeding.
- Drawings from all consultants relating to the same area should be read in conjunction with one another.
- Should the contractor discern any conflicting information written or drawn, he is to notify the architect immediately.
- This drawing is subject to world copyright and may not be reproduced in whole or in part for any purpose without prior written consent Allcrownworks.

CLIENT.
MR OKUNOWO OMOLADE TOSIN.

PROJECT NAME AND ADDRESS.
PROPOSED RESIDENTIAL BUILDING PROJECT
@ 22 SUNNY CLOSE,
DELE ADEDUGBE ESTATE,
FORMER WILLIAMS ELLIOT ESTATE,
NEW OKO-OBA,
IFAKO-IJAIYE LOCAL GOVT AREA,
LAGOS STATE.

DRAWING TITLE	DIMENSION.	
DATE	JANUARY 2024.	
DESIGNED BY	ARCH TAYO CHARLES ADEDAPO.	TEL: +2348033574252.
DRAWN BY	ALLCROWNWORKS.	TEL: +2348071070888, +2348120156282.
CHECKED BY	ARCH TAYO CHARLES ADEDAPO.	
SCALE	SCALE TO FIT.	SHEET D2

GENERAL NOTE.		
NO.	REVISION ISSUE	DATE

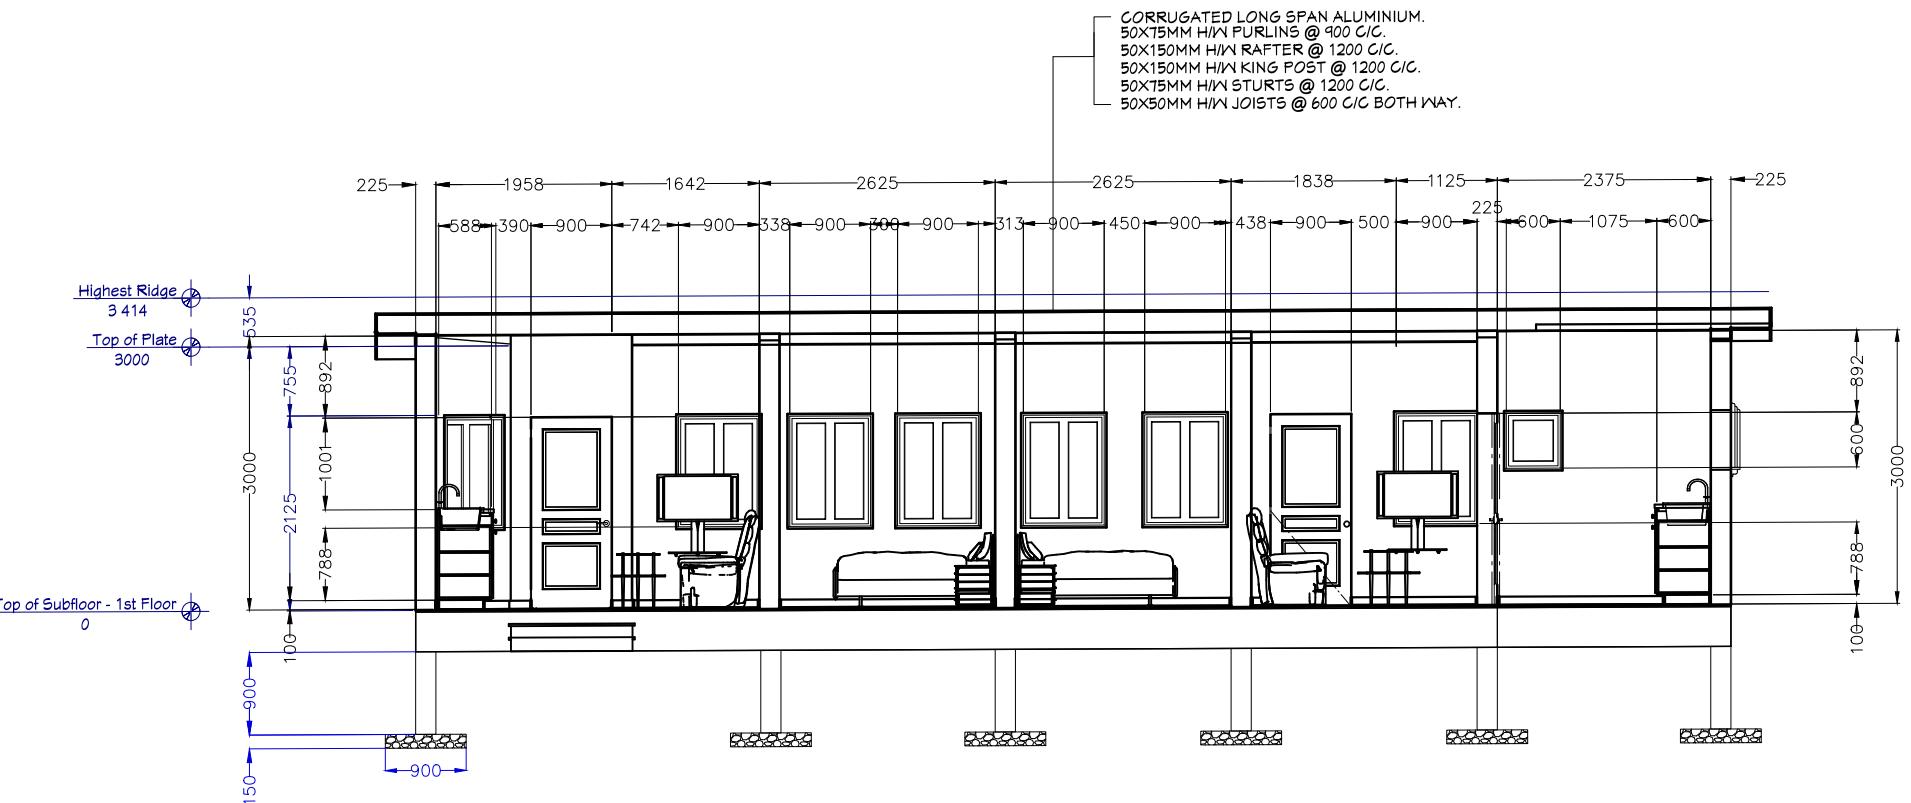

GENERAL NOTE.

1. Dimensions are to be read and not scaled.
2. All dimensions and conditions are to be verified on site before proceeding.
3. Drawings from all consultants relating to the same area should be read in conjunction with one another.
4. Should the contractor discern any conflicting information written or drawn, he is to notify the architect immediately.
5. This drawing is subject to world copyright and may not be reproduced in whole or in part for any purpose without prior written consent Allcrownworks.

CLIENT.
MR OKUNOWO OMOLADE TOSIN.


PROJECT NAME AND ADDRESS.
PROPOSED RESIDENTIAL BUILDING PROJECT
 @ 22 SUNNY CLOSE,
 DELE ADEDUBBE ESTATE,
 FORMER WILLIAMS ELLIOT ESTATE,
 NEW OKO-OBA,
 IFAKO-IIAJYE LOCAL GOVT AREA,
 LAGOS STATE.

DRAWING TITLE	SECTION X.
DATE	JANUARY 2024.
DESIGNED BY	ARCH TAYO CHARLES ADEDAOPO. TEL: +2348033574252.
DRAWN BY	ALLCROWNWORKS. TEL: +2348071070888, +2348120156282.
CHECKED BY	ARCH TAYO CHARLES ADEDAOPO.
SCALE	SCALE TO FIT.
SHEET D3	

GENERAL NOTE.

NO.	REVISION ISSUE	DATE

CORRUGATED LONG SPAN ALUMINIUM.
 50X75MM H/W PURLINS @ 900 C/C.
 50X150MM H/W RAFTER @ 1200 C/C.
 50X150MM H/W KING POST @ 1200 C/C.
 50X75MM H/W STURTS @ 1200 C/C.
 50X50MM H/W JOISTS @ 600 C/C BOTH WAY.

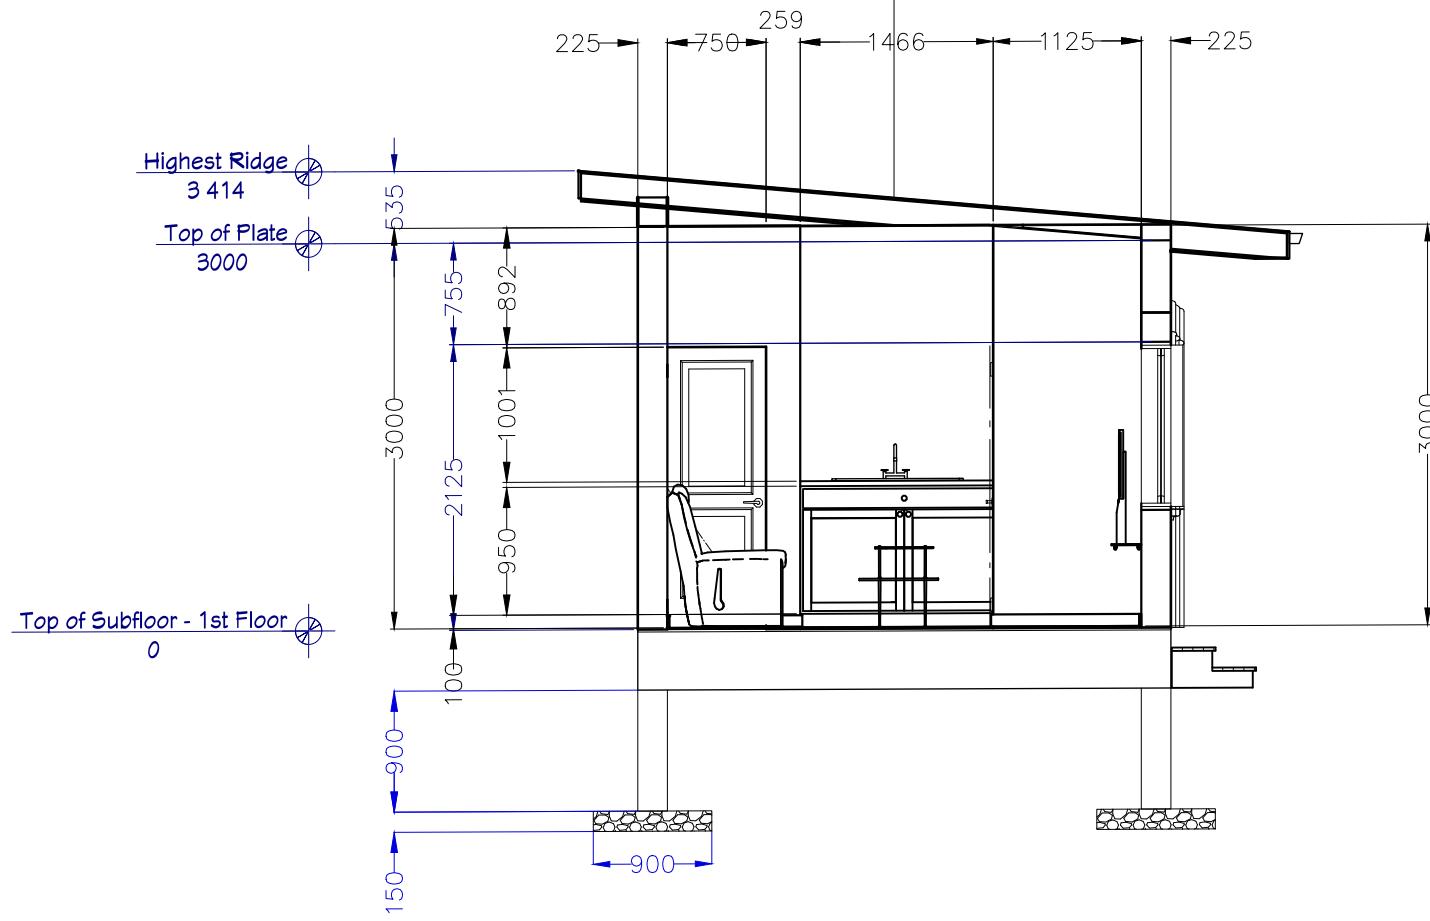

GENERAL NOTE.
 1. Dimensions are to be read and not scaled.
 2. All dimensions and conditions are to be verified on site before proceeding.
 3. Drawings from all consultants relating to the same area should be read in conjunction with one another.
 4. Should the contractor discern any conflicting information written or drawn, he is to notify the architect immediately.
 5. This drawing is subject to world copyright and may not be reproduced in whole or in part for any purpose without prior written consent Allcrownworks.


CLIENT.
MR OKUNOWO OMOLADE TOSIN.

PROJECT NAME AND ADDRESS.
PROPOSED RESIDENTIAL BUILDING PROJECT
 @ 22 SUNNY CLOSE,
 DELE ADEDUGBE ESTATE,
 FORMER WILLIAMS ELLIOT ESTATE,
 NEW OKO-OBA,
 IFAKO-IJAYE LOCAL GOVT AREA,
 LAGOS STATE.

DRAWING TITLE	SECTION Y.
DATE	JANUARY 2024.
DESIGNED BY	ARCH TAYO CHARLES ADEDAO.
DRAWN BY	ALLCROWNWORKS.
CHECKED BY	ARCH TAYO CHARLES ADEDAO.
SCALE	SCALE TO FIT.
SHEET D4	

GENERAL NOTE.

NO.	REVISION ISSUE	DATE
-----	----------------	------

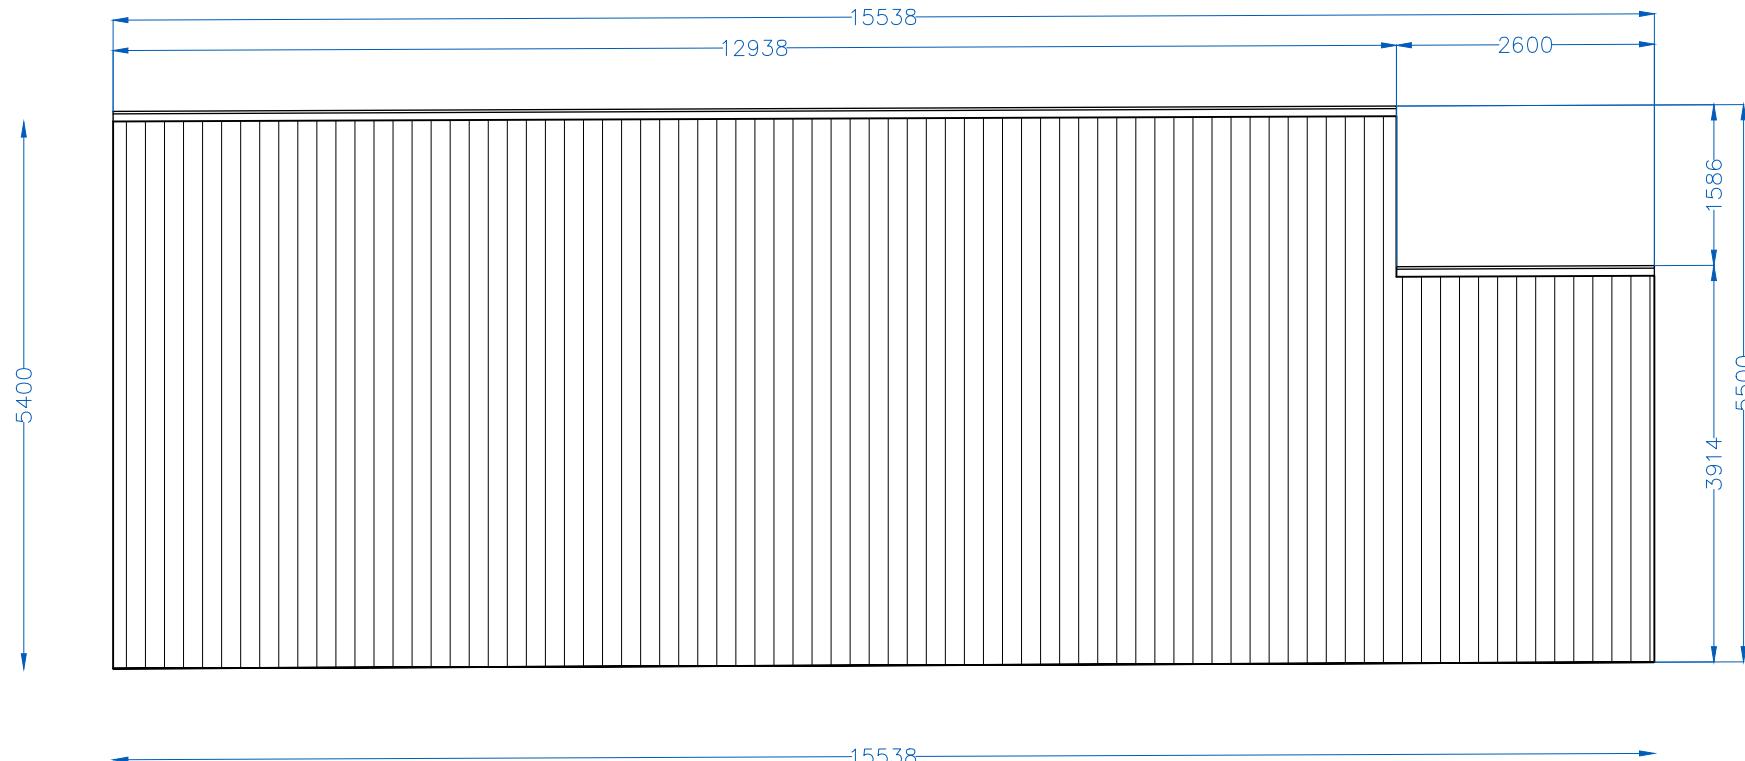

GENERAL NOTE.

- Dimensions are to be read and not scaled.
- All dimensions and conditions are to be verified on site before proceeding.
- Drawings from all consultants relating to the same area should be read in conjunction with one another.
- Should the contractor discern any conflicting information written or drawn, he is to notify the architect immediately.
- This drawing is subject to world copyright and may not be reproduced in whole or in part for any purpose without prior written consent Allcrownworks.

CLIENT.

MR OKUNOWO OMOLADE TOSIN.


PROJECT NAME AND ADDRESS.

PROPOSED RESIDENTIAL BUILDING PROJECT


© 22 SUNNY CLOSE,
DELE ADEDUGBE ESTATE,
FORMER WILLIAMS ELLIOT ESTATE,
NEW OKO-OBA,
IFAKO-IIAJYE LOCAL GOVT AREA,
LAGOS STATE.

DRAWING TITLE	ROOF.
DATE	JANUARY 2024.
DESIGNED BY	ARCH TAYO CHARLES ADEDAPO. TEL: +2348033574252.
DRAWN BY	ALLCROWNWORKS. TEL: +2348071070888, +2348120156282.
CHECKED BY	ARCH TAYO CHARLES ADEDAPO.
SCALE	SCALE TO FIT.
	SHEET D5

GENERAL NOTE.		
NO.	REVISION ISSUE	DATE

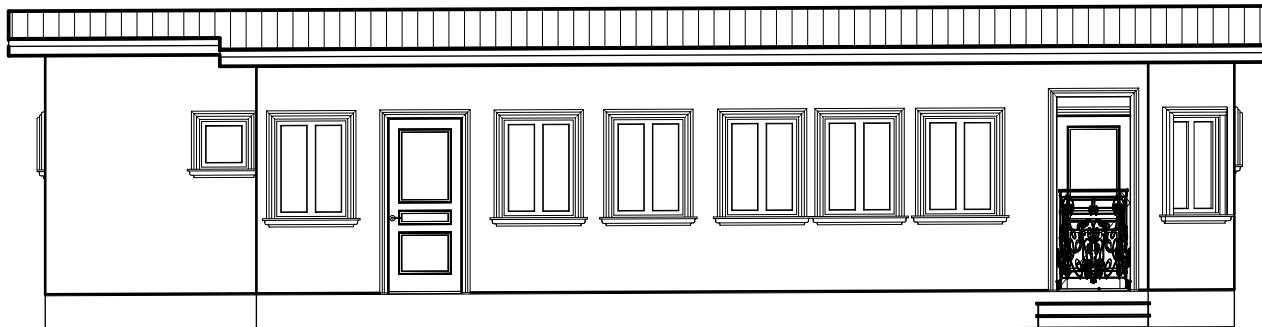

FRONT SIDE VIEW

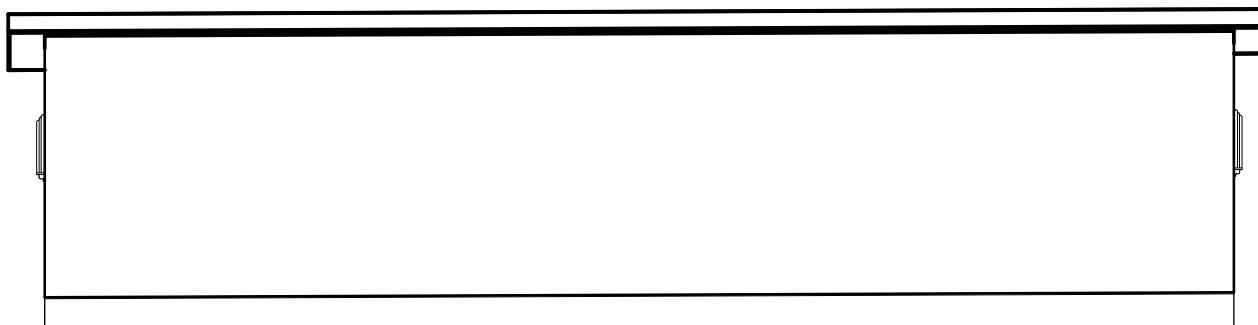

REAR VIEW



ARCHITECTURE ITEM NAME AND ADDRESS.

3A, ANIFOWOSHE STREET, ABULE EGBA IFAKO IJAYE, LAGOS

GENERAL NOTE:

1. Dimensions are to be read and not scaled.
2. All dimensions and conditions are to be verified on site before proceeding.
3. Drawings from all consultants relating to the same area should be read in conjunction with one another.
4. Should the contractor discern any conflicting information written or drawn, he is to notify the architect immediately.
5. This drawing is subject to world copyright and may not be reproduced in whole or in part for any purpose without prior written consent Allcrownworks.

CLIENT.

MR OKUNOWO OMOLADE TOSIN.

PROJECT NAME AND ADDRESS.

PROPOSED RESIDENTIAL BUILDING PROJECT
@
22 SUNNY CLOSE,
DELE ADEDUKE ESTATE,
FORMER WILLIAMS ELLIOT ESTATE,
NEW OKO-OBA,
IFAKO-IJAYE LOCAL GOVT AREA,
LAGOS STATE.

DRAWING TITLE FRONT AND REAR VIEW.

DATE JANUARY 2024.

DESIGNED BY ARCH TAYO CHARLES ADEDAPO.
TEL: +2348033574252.


DRAWN BY ALLCROWNWORKS.
TEL: +2348071070888, +2348120156282.

CHECKED BY ARCH TAYO CHARLES ADEDAPO.


SCALE SCALE TO FIT. SHEET D6

GENERAL NOTE.

NO.	REVISION/ISSUE	DATE

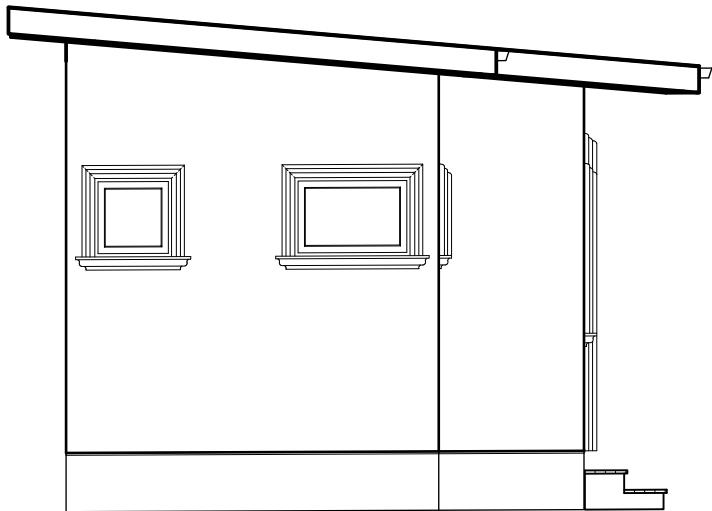

LEFT SIDE VIEW

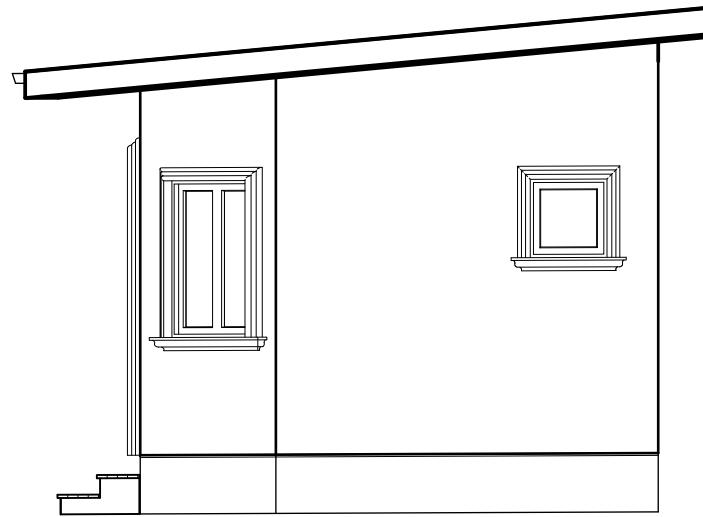


RIGHT SIDE VIEW




ARCHITECTURE FIRM NAME AND ADDRESS.

3A, ANIFOWOSHE STREET, ABULE EGBA IFAKO IJAYE, LAGOS

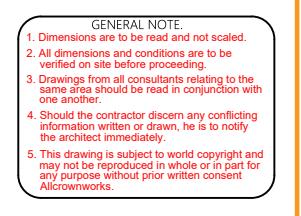

GENERAL NOTE:

- Dimensions are to be read and not scaled.
- All dimensions and conditions are to be verified on site before proceeding.
- Drawings from all consultants relating to the same area should be read in conjunction with one another.
- Should the contractor discern any conflicting information written or drawn, he is to notify the architect immediately.
- This drawing is subject to world copyright and may not be reproduced in whole or in part for any purpose without prior written consent Allcrownworks.

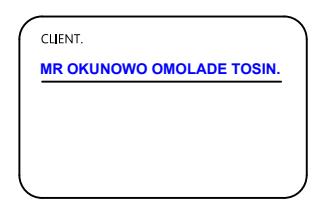


CLIENT.

MR OKUNOWO OMOLADE TOSIN.



PROJECT NAME AND ADDRESS.

PROPOSED RESIDENTIAL BUILDING PROJECT
@
22 SUNNY CLOSE,
DELE ADEDUGBE ESTATE,
FORMER WILLIAMS ELLIOT ESTATE,
NEW OKO-OBA,
IFAKO-IJAYE LOCAL GOVT AREA,
LAGOS STATE.

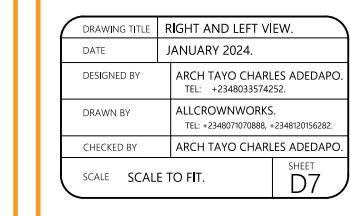

DRAWING TITLE: RIGHT AND LEFT VIEW.

DATE: JANUARY 2024.

DESIGNED BY: ARCH TAYO CHARLES ADEDAPO.

TEL: +2348033574252.


DRAWN BY: ALLCROWNWORKS.

TEL: +2348071070888, +2348120156282.

CHECKED BY: ARCH TAYO CHARLES ADEDAPO.

SCALE: SCALE TO FIT.

SHEET: D7

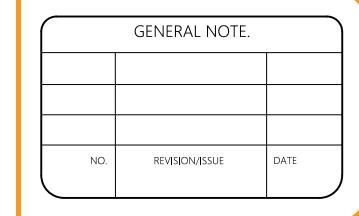

GENERAL NOTE.

NO.	REVISION/ISSUE	DATE